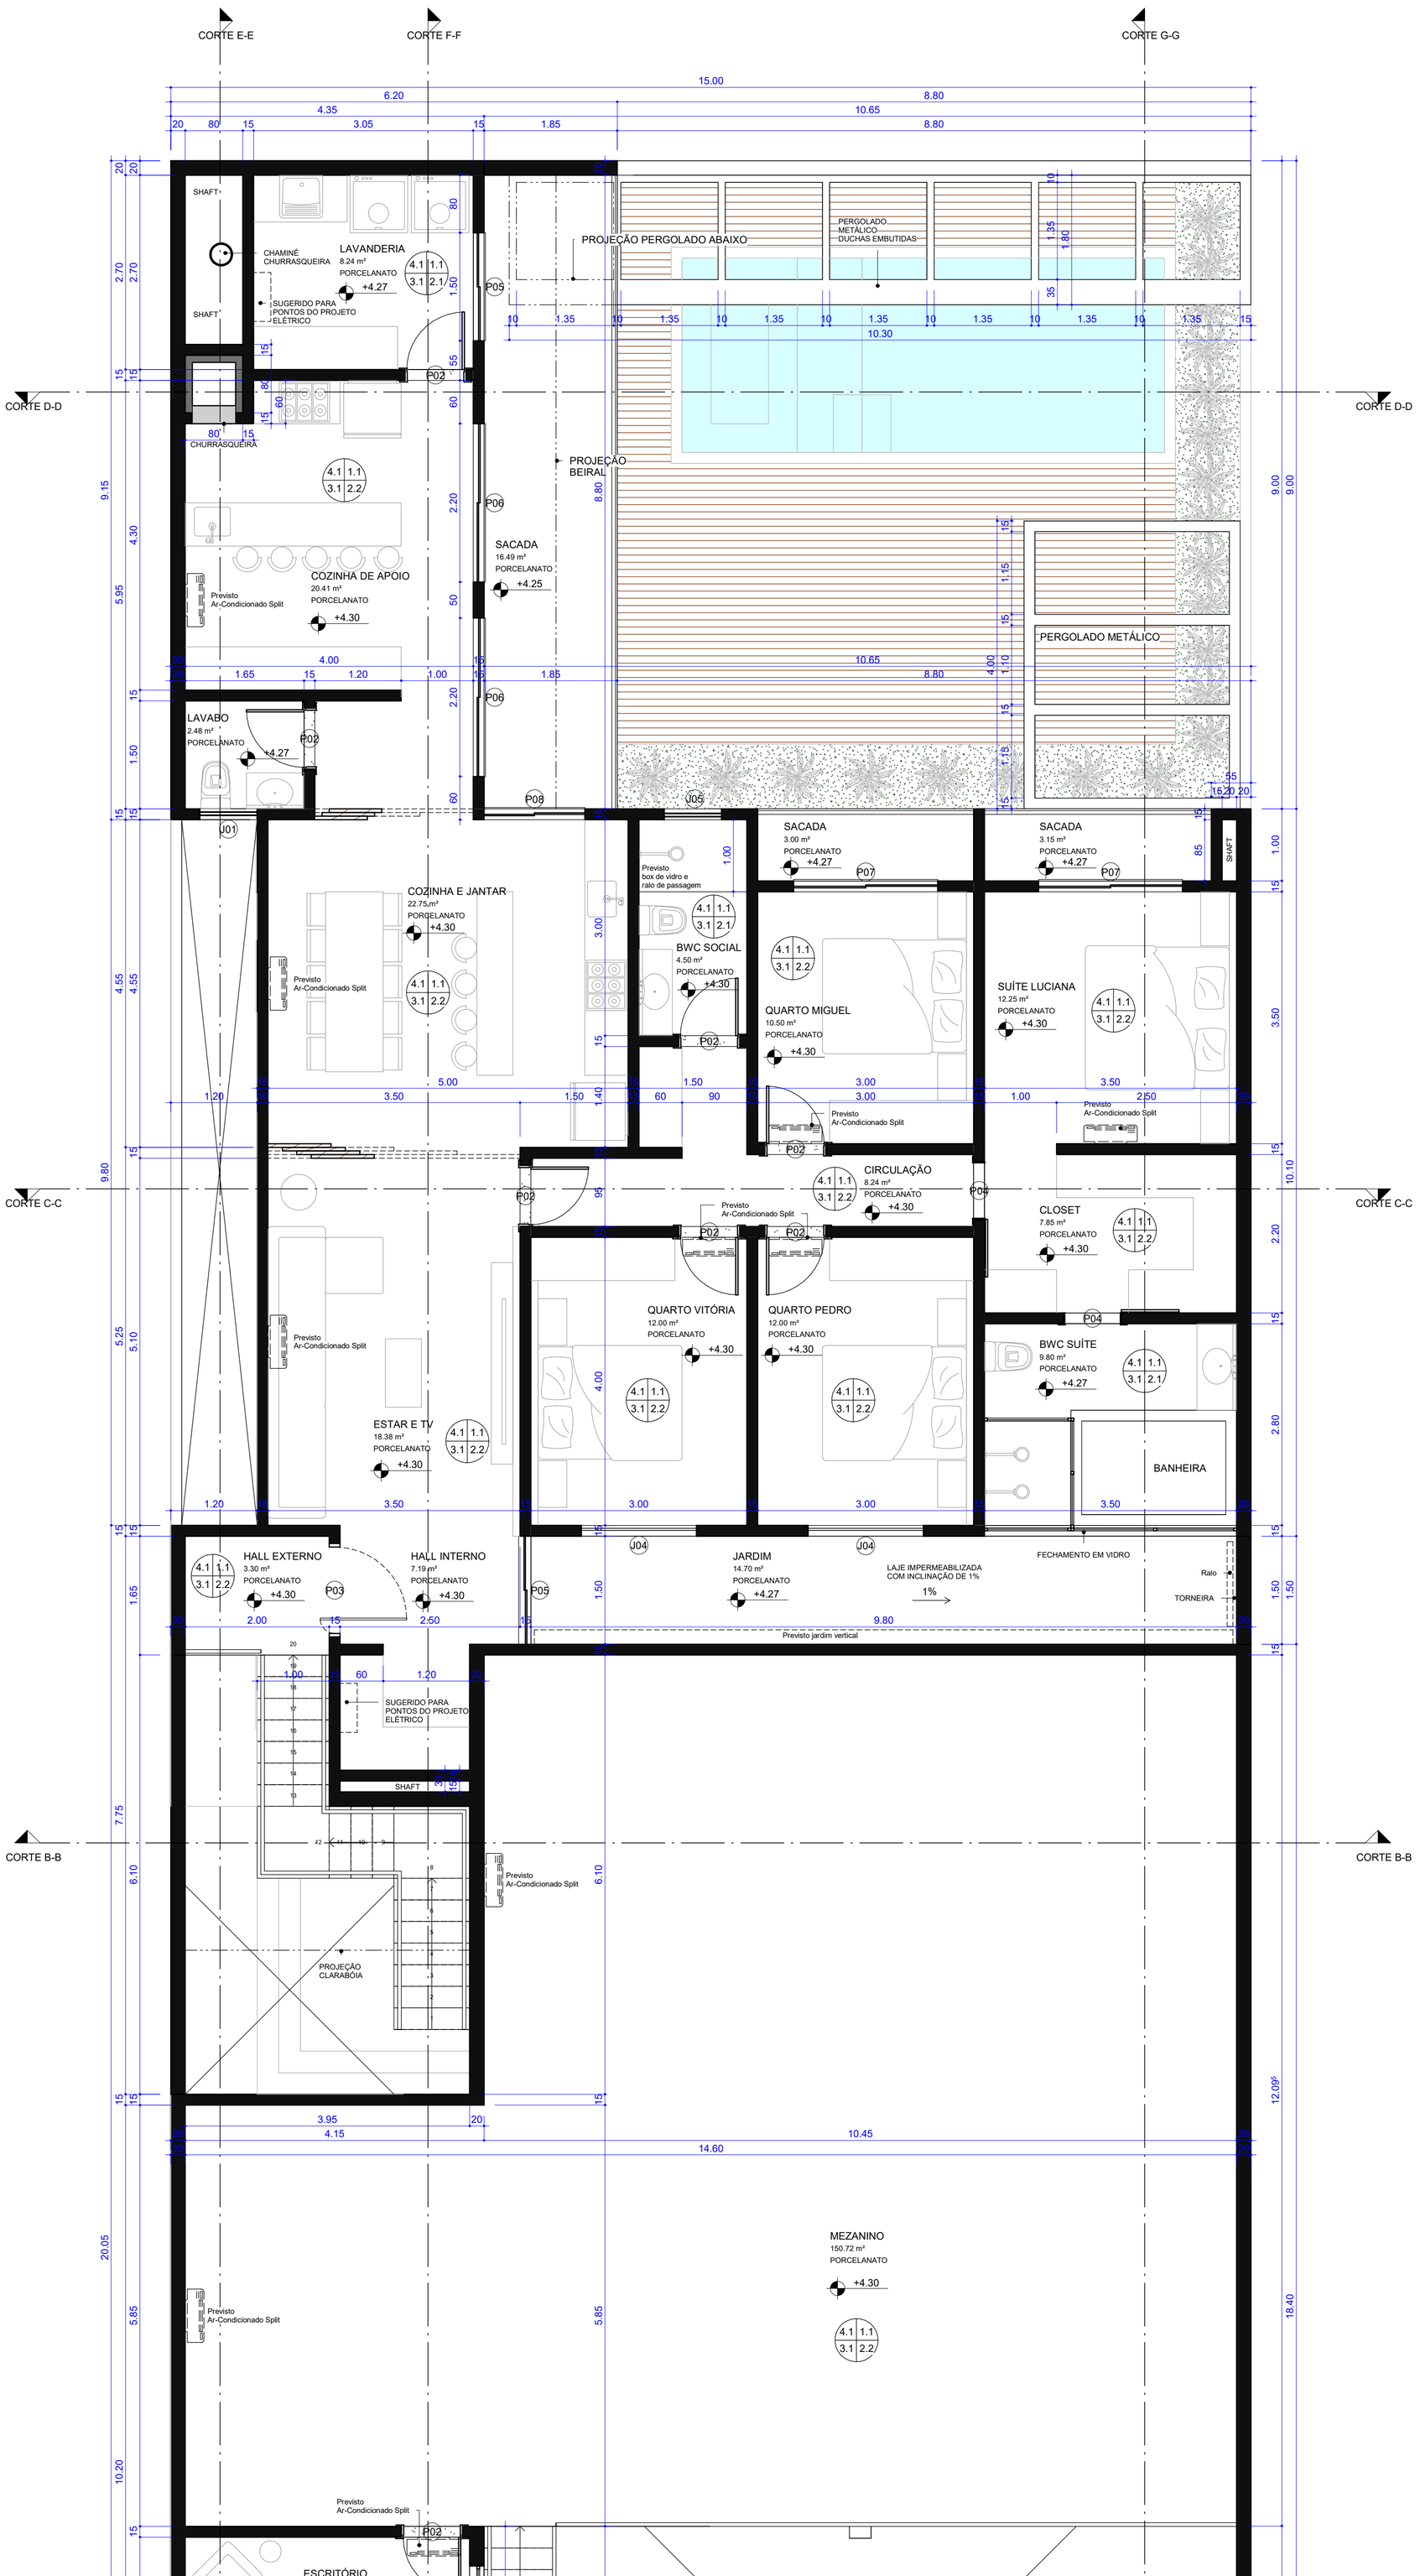


1 PLANTA BAIXA PAV. SUPERIOR
ESCALA 1 : 50

NOTAS GERAIS:

1. TODAS AS MEDIDAS DEVERÃO SER CONFERIDAS NA OBRA.

2. O PROJETO ESTÁ DE ACORDO COM AS NORMAS E LEGISLAÇÃO RELATIVAS À NBR 13532/1995 - ELABORAÇÃO DE PROJETOS DE EDIFICAÇÕES DE ARQUITETURA E NBR 6492/1994 - REPRESENTAÇÃO DE PROJETOS DE ARQUITETURA.

3. O DIMENSIONAMENTO DE CALHAS, RUFOS E AFINS DEVERÃO SER CONFERIDOS JUNTAMENTE COM O PROJETO DE ÁGUAS PLUVIAIS.

4. AS ÁGUAS DAS COBERTURAS DEVERÃO TER INCLINAÇÃO DE CONFORME ESPECIFICADO EM PROJETO.

5. VER PROJETOS ESPECÍFICOS DE ESTRUTURA E INSTALAÇÕES DE ELÉTRICA (ILUMINAÇÃO, TOMADAS E ALIMENTADORES), HIDRAULICA (ÁGUA FRIA E QUENTE, ESGOTO E ALIMENTADORES).

6. MEDIDAS DE PROJETO EM METROS.

LEGENDA DE ACABAMENTOS

4 | 1
3 | 2
1- PISO
2- PAREDES
3- FORRO
4- RODAPÉS

1- PISO
1.1 PORCELANATO ACETINADO OU POLIDO, 75X75CM, ESP. 10MM (A DEFINIR COR), JUNTA 3MM, REJUNTE (A DEFINIR COR) RESISTENTE A FUNGOS E MOFOS.

2- PAREDES
2.1 REVESTIMENTO EM PORCELANATO POLIDO COR BRANCO, 75X75CM, ESP. 10MM, JUNTA 3MM, REJUNTE BRANCO, RESISTENTE A FUNGOS E MOFOS.
2.2 PINTURA EM TINTA ACRÍLICA ACETINADA NA COR BRANCO REFERÊNCIA "SUVINIL - BRANCO PURO - N501" OU SIMILIAR/EQUIVALENTE OU DE QUALIDADE SUPERIOR, APLICADO SOBRE CHAPISCO, REBOCO, EMBOÇO E MASSA ACRÍLICA.

3- FORRO
3.1 FORRO EM GESSO ACARTONADO LISO COM PINTURA EM TINTA PVA FOSCA NA COR BRANCO REFERÊNCIA "SUVINIL - BRANCO PURO - N501" OU SIMILIAR/EQUIVALENTE OU DE QUALIDADE SUPERIOR, APLICADO SOBRE MASSA PVA.

4- RODAPÉS
4.1 PORCELANATO ACETINADO OU POLIDO, 15CM DE ALT. ESP. 10MM, (A DEFINIR COR) JUNTA 3MM, REJUNTE (A DEFINIR COR), RESISTENTE A FUNGOS E MOFOS.

PARA OS PROJETOS DE INSTALAÇÕES

- ASPECTOS PARA PROJETO HIDROSSANITÁRIO

PROJETO ARQUITETÔNICO COM OS PONTOS DE UTILIZAÇÃO **(DEFINIDO E APROVADO)**

PONTO DE ALIMENTAÇÃO DA ÁGUA POTÁVEL EM PROJETO **(VER PLANTA TÉRREO OU IMPLANTAÇÃO)**

SISTEMAS A SEREM UTILIZADOS NESSA OBRA **(ÁGUA FRIA, ÁGUA QUENTE, PISCINA AQUECIDA)**

SISTEMA DE TRATAMENTO DE ESGOTO **(FOSSA SÉPTICA)**

SISTEMA DE DESAGUE DE ÁGUAS PLUVIAIS **(SARJETA)**

SISTEMA DE AQUECIMENTO DE ÁGUA **(BOILER ELÉTRICO PARA ÁREA RESIDENCIAL E PLACA SOLAR PARA PISCINA)**

POSIÇÃO DAS COLUNAS DOS SISTEMAS **(SHAFT)**

ACIONAMENTO DE BACIAS SANITÁRIAS **(CAIXA ACOPLADA)**

REGISTRO PARA CHUVEIROS **(MISTURADOR MONOCOMANDO)**

PONTO PARA TORNEIRA DE JARDIM **(PONTO SUGERIDO)**

PONTO PARA CASA DE MÁQUINAS **(PONTO SUGERIDO)**

PONTO DO EVAPORADOR DE AR-CONDICIONADO **(PONTO SUGERIDO)**

PONTO DE RESERVATÓRIO SUPERIOR **(VOLUME CAIXA D'ÁGUA)**

- ASPECTOS PARA PROJETO ELÉTRICO

PROJETO ARQUITETÔNICO COM LAYOUT **(DEFINIDO E APROVADO)**

SISTEMAS A SEREM UTILIZADOS NESSA OBRA **(ENERGIA, LÓGICA, CFTV, CABEAMENTO, SPDA, AR CONDICIONADO)**

PROJETO LUMINOTÉCNICO COM ESPECIFICAÇÃO DE LUMINÁRIAS **(NÃO POSSUI)**

PONTO DE MEDIÇÃO E LEITURA **(SHAFT FRONTAL)**

PONTO DO EVAPORADOR E CONDENSADOR DO AR-CONDICIONADO **(PONTO SUGERIDO)**

PONTO DO QUADRO DE DISTRIBUIÇÃO **(PONTO SUGERIDO)**

PONTO DO QUADRO DE LÓGICA **(PONTO SUGERIDO)**

PONTO DE USO GERAL (A DEFINIR)

PONTO DE USO ESPECÍFICO (A DEFINIR)

PONTO PARA INVERSOR E STRING BOX (UFV – ENERGIA SOLAR) **(PONTO SUGERIDO)**

PONTO PARA CASA DE MÁQUINAS **(PONTO SUGERIDO)**

- ASPECTOS A SEREM VERIFICADOS DO PROJETO DE GÁS

POSIÇÃO DA CENTRAL DE GLP **(PONTO SUGERIDO)**

QUANTITATIVO DE PORTAS.

CÓD	QT	LARGURA	ALTURA	DESCRIÇÃO
P01	1	2.97 m	3.00 m	PORTÃO BASCULANTE DE ALUMÍNIO C/ PINTURA CINZA
P02	17	0.80 m	2.10 m	PORTA DE ABRIR DE MADEIRA
P03	1	1.20 m	2.85 m	PORTA PIVOTANTE DE MADEIRA
P04	2	0.80 m	2.10 m	PORTA DE CORRER DE MADEIRA
P05	2	1.50 m	2.50 m	PORTA DE CORRER DE VIDRO 2 FOLHAS
P06	2	2.20 m	2.50 m	PORTA DE CORRER DE VIDRO 3 FOLHAS
P07	2	2.00 m	2.50 m	PORTA DE CORRER DE VIDRO 3 FOLHAS
P08	1	1.40 m	2.50 m	PORTA DE CORRER DE VIDRO 2 FOLHAS
Grand total: 28				

QUANTITATIVO DE JANELAS.

CÓD	QT	COMPRIMENTO	ALTURA	PEITORIL	DESCRIÇÃO
J01	3	0.80 m	0.60 m	1.60 m	JANELA DE CORRER DE VIDRO ESQUADRIA DE ALUMÍNIO
J02	2	1.20 m	1.00 m	1.00 m	JANELA DE CORRER DE VIDRO ESQUADRIA DE ALUMÍNIO
J03	1	0.80 m	0.50 m	2.50 m	JANELA DE CORRER DE VIDRO ESQUADRIA DE ALUMÍNIO
J04	2	1.60 m	1.00 m	1.10 m	JANELA DE CORRER DE VIDRO ESQUADRIA DE ALUMÍNIO
J05	1	0.80 m	0.90 m	1.60 m	JANELA DE CORRER DE VIDRO ESQUADRIA DE ALUMÍNIO
J06	1	3.00 m	0.80 m	1.00 m	JANELA DE CORRER DE VIDRO ESQUADRIA DE ALUMÍNIO
J07	1	1.60 m	0.80 m	1.00 m	JANELA DE CORRER DE VIDRO ESQUADRIA DE ALUMÍNIO

TÍTULO DA PRANCHA: PROJETO DE ARQUITETURA COMERCIAL E RESIDENCIAL
PRANCHA: 02/07
ESCALAS: INDICADA
CONTEÚDO: PLANTA BAIXA PAV. SUPERIOR
USO DA EDIFICAÇÃO: COMERCIAL E RESIDENCIAL
TIPO: CONSTRUÇÃO
COEF. DE APROVEITAM.: 1,43
ÁREA PERMEAVEL (%): 16,38
TAXA DE OCUPAÇÃO (%): 81,91
LOCAL DA OBRA: RUTA N" 03 "AV. DE LAS RESIDENTAS " LA PALOMA - CANINDEYU PARAGUAY
QUADRA"X" LOTE XX
DATA DO PROJETO: 30/12/2024 10:29:49
REVISÃO: 00
NÚMERO DO PROJETO: 000/0000/000
CPF/CNPJ PROPRIETÁRIO (A): 000.000.000-00
DECLARO QUE A APROVAÇÃO DO PROJETO NÃO IMPLICA NO RECONHECIMENTO PELA PREFEITURA DO DIREITO DE PROPRIEDADE DO TERRENO
PROPRIETÁRIO (A): LUCIANA MOREIRA FERMINO

GABRIEL FERMINO

QUADRO DE ÁREAS (m²)
ÁREA TERRENO 600m²
ÁREA TÉRREO 491,44m²
ÁREA SUPERIOR 372,10m²
ÁREA PISCINA 21m²
ÁREA CALÇADAS 10,30m²
ÁREA TOTAL A CONSTRUIR 863,54m²

ESPAÇO RESERVADO PARA APROVAÇÃO

Observações:
NOTAS:

a) É mandatório o perfeito entendimento dos projetos antes da sua execução, em caso de dúvida consultar o autor do projeto

b) Vedada a reprodução, alteração ou cópia, total ou parcial, sem a autorização expressa do autor.