

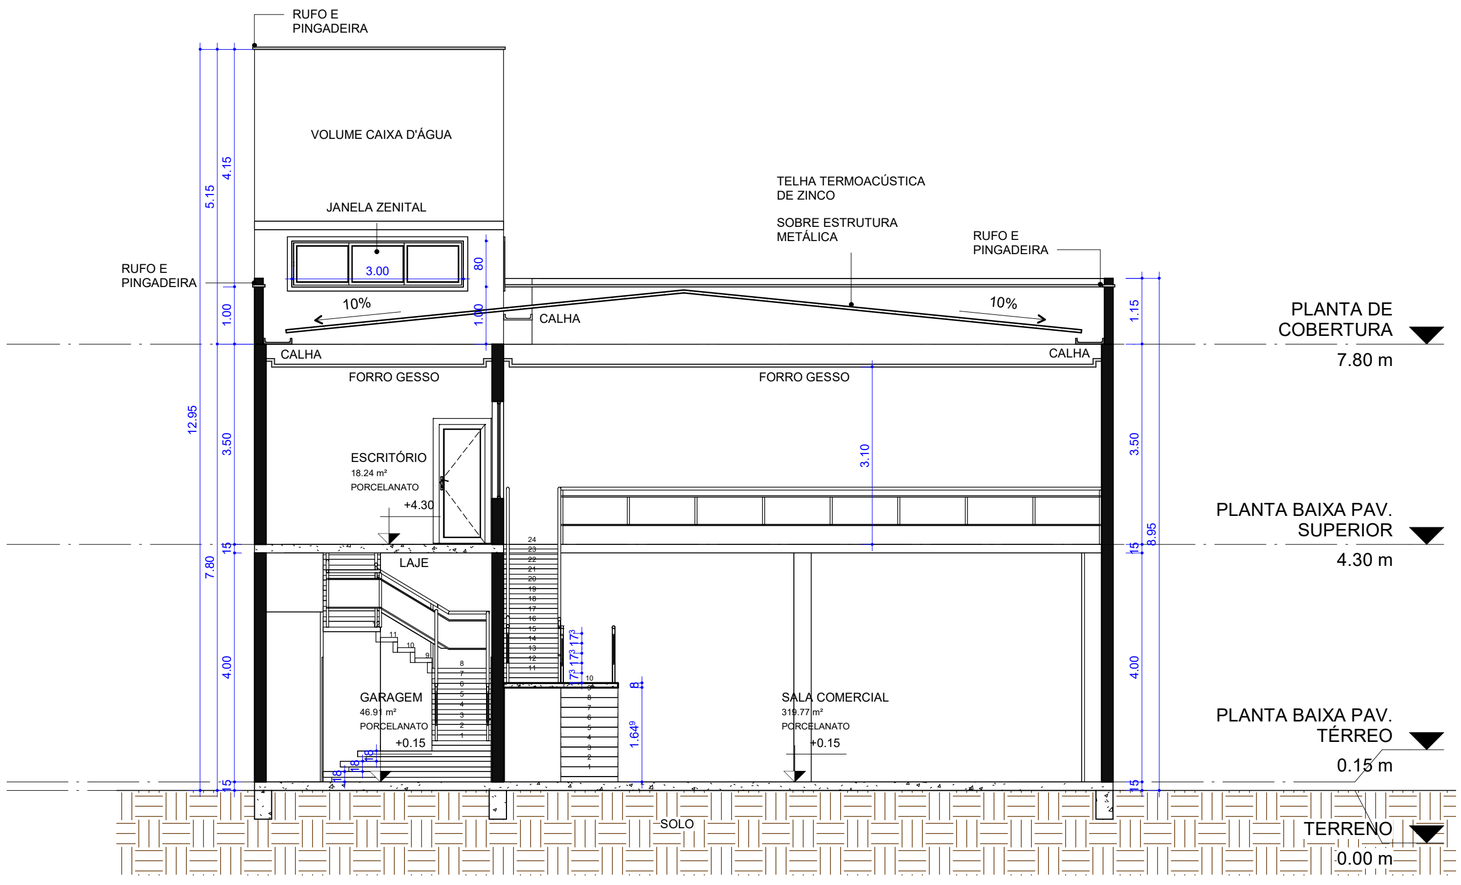


1 CORTE A-A
ESCALA 1 : 75

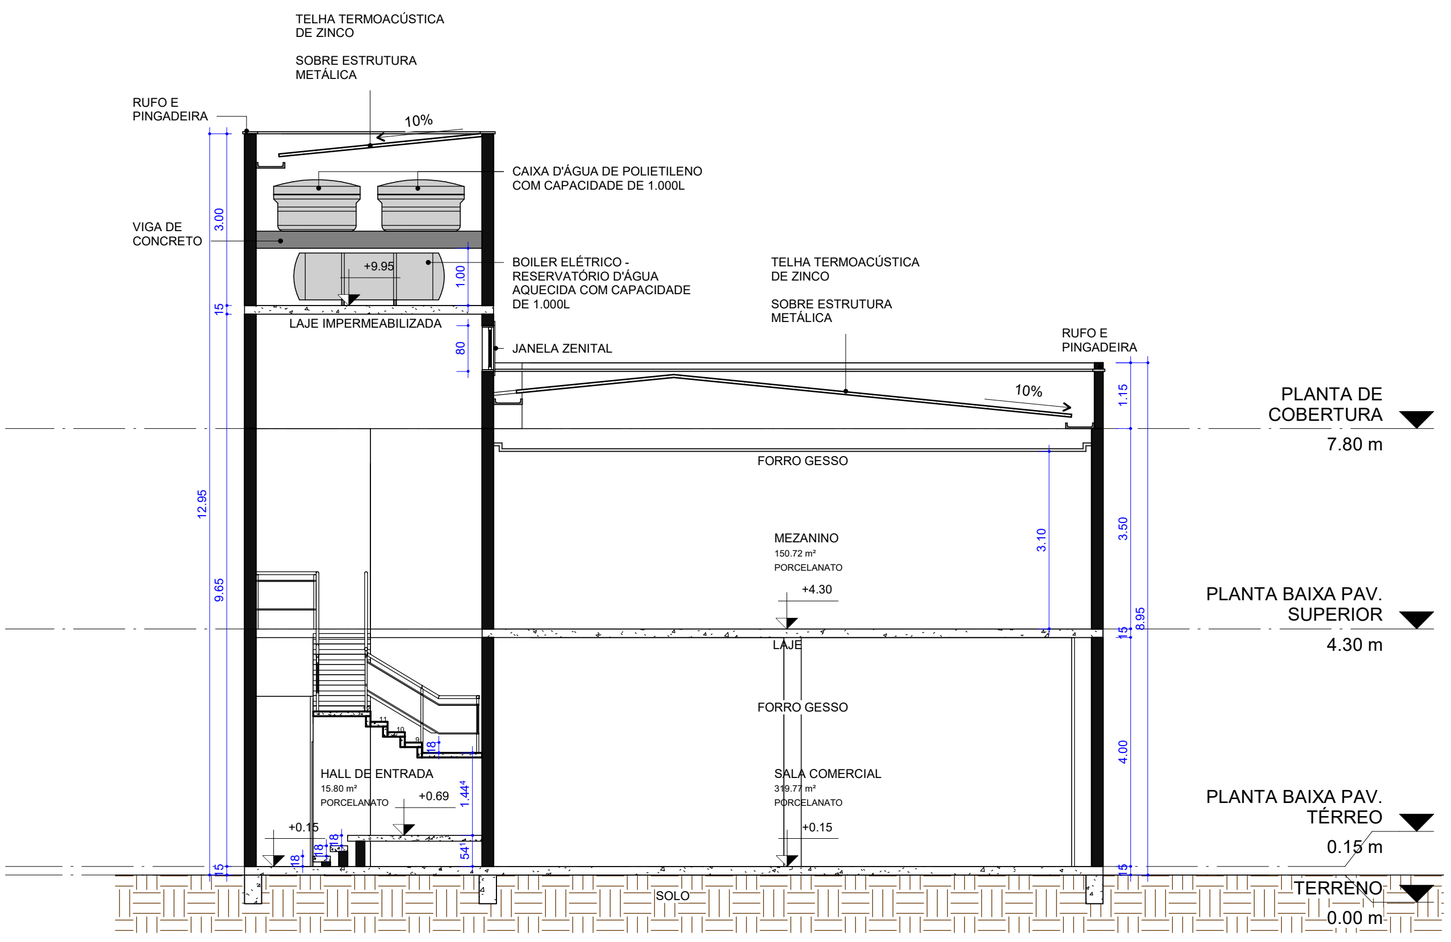

2 CORTE B-B
ESCALA 1 : 75

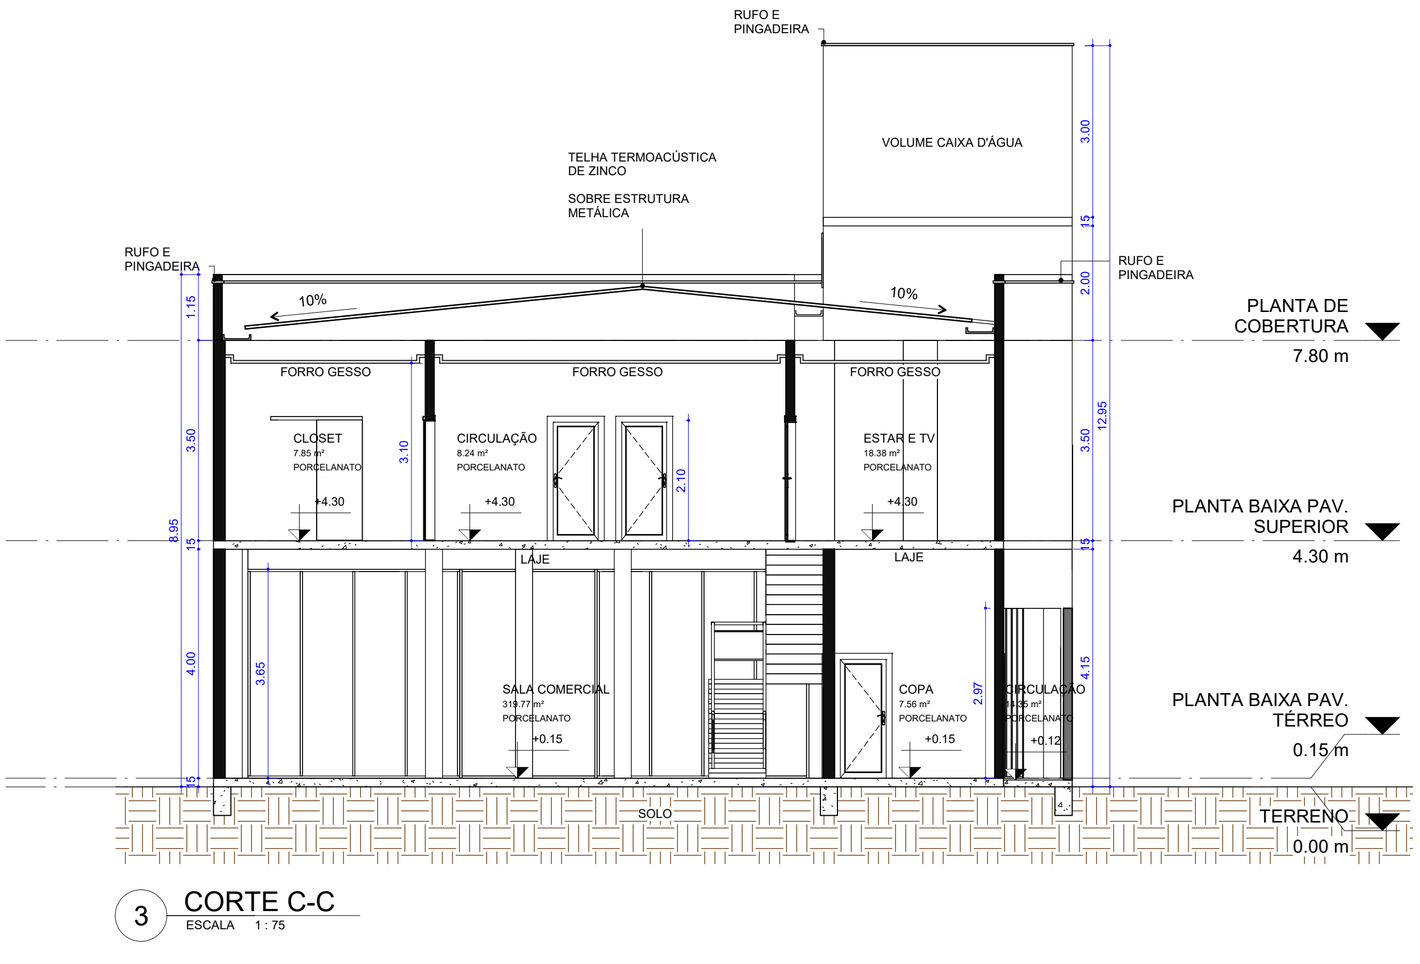

3 CORTE C-C
ESCALA 1 : 75

4 CORTE D-D
ESCALA 1 : 75

TÍTULO DA PRANCHA PROJETO DE ARQUITETURA COMERCIAL E RESIDENCIAL		PRANCHA **05/07**	ESCALAS INDICADA
CONTEÚDO CORTE A-A CORTE B-B CORTE C-C CORTE D-D	USO DA EDIFICAÇÃO **COMERCIAL E RESIDENCIAL**	TIPO CONSTRUÇÃO	COEF. DE APROVEITAM. 1,43
LOCAL DA OBRA RUTA N" 03 "AV. DE LAS RESIDENTAS " LA PALOMA - CANINDEYU PARAGUAY	QUADRA"X" LOTE XX	DATA DO PROJETO 30/12/2024 10:32:07	ÁREA PERMEAVEL (%) 16,38 TAXA DE OCUPAÇÃO (%) 81,91
REVISÃO **00**		NÚMERO DO PROJETO 000/0000/000	
		CPF/CNPJ PROPRIETÁRIO (A) 000.000.000-00	

GABRIEL FERMINO

DECLARO QUE A APROVAÇÃO DO PROJETO NÃO IMPLICA NO RECONHECIMENTO PELA PREFEITURA DO DIREITO DE PROPRIEDADE DO TERRENO

PROPRIETÁRIO (A)
LUCIANA MOREIRA FERMINO

QUADRO DE ÁREAS (m²)

ÁREA TERRENO 600m²
ÁREA TÉRREO 491,44m²
ÁREA SUPERIOR 372,10m²

ÁREA PISCINA 21m²
ÁREA CALÇADAS 10,30m²

ÁREA TOTAL A CONSTRUIR 863,54m²

ESPAÇO RESERVADO PARA APROVAÇÃO

Observações:
NOTAS:

a) É mandatório o perfeito entendimento dos projetos antes da sua execução, em caso de dúvida consultar o autor do projeto

b) Vedada a reprodução, alteração ou cópia, total ou parcial, sem a autorização expressa do autor.