
GABRIEL FERMINO
ARQUITETURA

LUCIANA

PAGINAÇÃO | OPÇÃO 90 × 90

Portinari 90 × 90 | Rejunte: 2 mm | Pavimento superior

PLANTA DE ASSENTAMENTO E RODAPÉS | 1:75

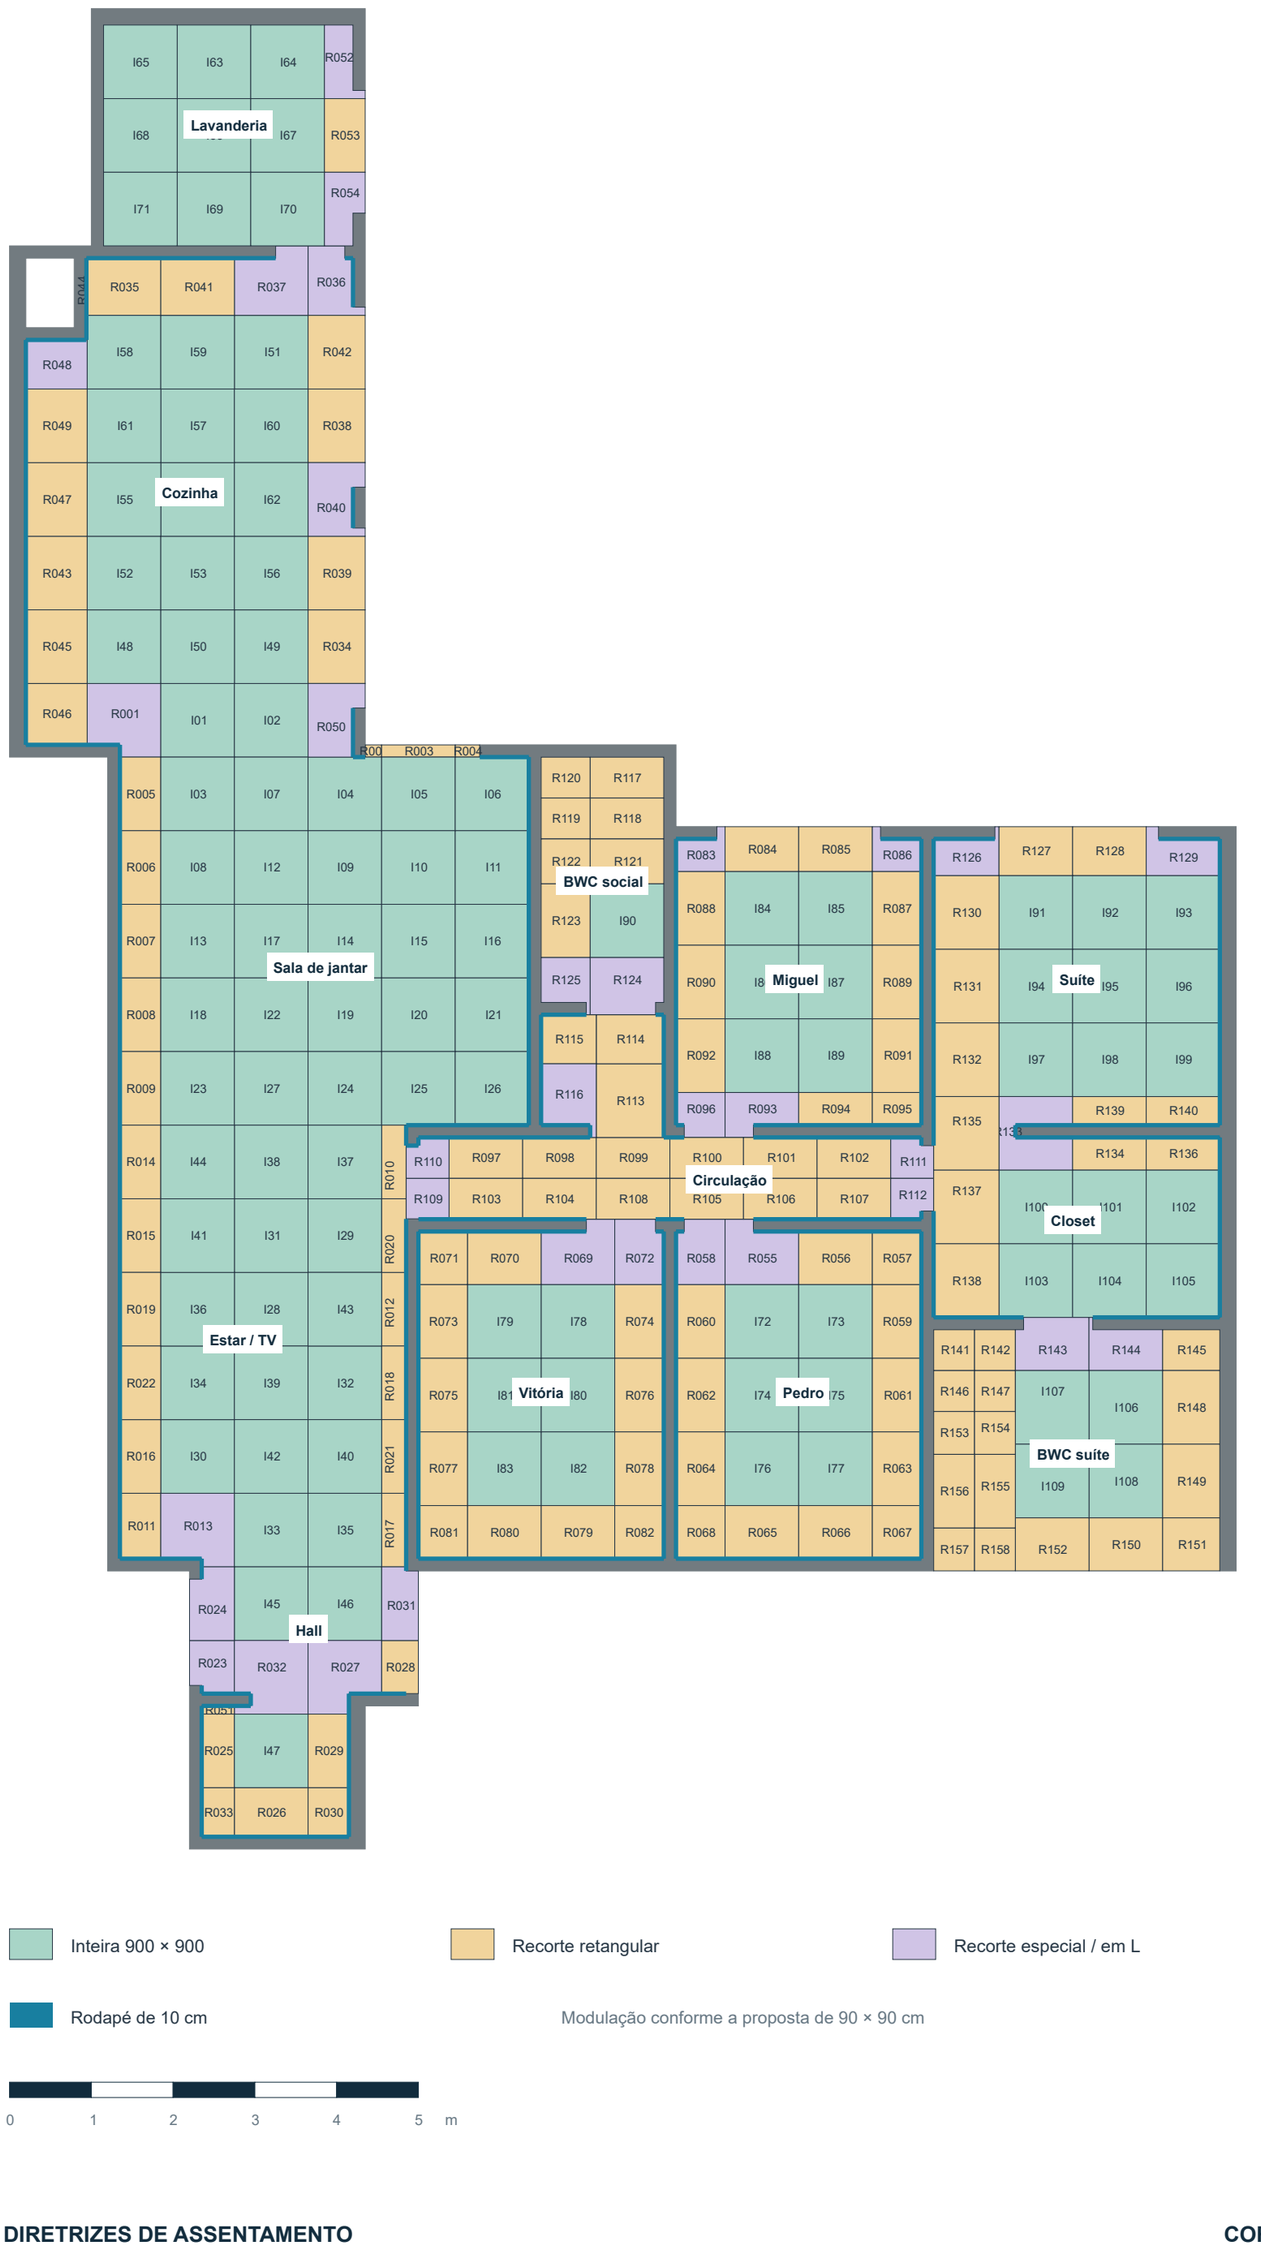

PISO LÍQUIDO	RODAPÉ 10 CM
160,54 m²	111,84 m

QUANTITATIVO POR AMBIENTE

AMBIENTE	INT.	REC.	m²	ROD. m
Social integrado	62	51	73,06	41,83
Suíte + closet	15	15	20,37	20,05
Quarto Miguel	6	14	10,90	10,15
Quarto Vitória	6	14	12,10	13,15
Quarto Pedro	6	14	12,10	13,15
Circulação	0	20	8,53	13,49
BWC social	1	9	4,61	-
BWC suíte	4	18	10,42	-
Lavanderia	9	3	8,46	-
TOTAL	**109**	**158**	**160,54**	**111,84**

CONSUMO E COMPRA

Placas inteiras	109
Placas para os recortes	138
Consumo total	247 placas | 200,07 m²
Reserva	13 placas | 10,53 m²
COMPRA	**260 placas | 210,60 m²**

Compra: 130 caixas de 1,62 m² ; confirmar embalagem, lote e dimensões efetivas.

APROVEITAMENTO

Rodapés: 11,18 m², em 163 peças, retiradas das sobras do piso. Nenhuma placa adicional no plano de corte.

Separar e identificar os retalhos conforme P02 e P03. As peças Bxx identificam os trechos de rodapé nas placas de origem.

DIRETRIZES DE ASSENTAMENTO

Malha contínua entre cozinha, sala de jantar, TV e hall; malha contínua entre suíte e closet. Distribuição dos recortes conforme a alternativa de 90 × 90 cm.

Rejunte: 2 mm. Folga perimetral: 5 mm. Peças nominais: 900 × 900 mm. Conferir dimensões reais e esquadros antes dos cortes.

Rodapés sem banheiros e lavanderia, descontados os vãos e as ombreiras. Marcenaria não descontada. Revestimentos de parede não incluídos.

CORTE E EXECUÇÃO

Serra considerada: 3 mm. Manter o sentido das peças do piso, sem rotação de 90°. Recortes em L: transferir por gabarito e conferir os cantos internos.

Conferir em obra ralos, caimentos e juntas estruturais e de movimentação. Conferir os recortes estreitos e as transições nas portas.

Índice: P01 planta e quantitativos; P02 e P03 cortes e aproveitamento; P04 dimensões dos recortes e origem dos rodapés. Imprimir a 100%.

Estimativa de aproveitamento - piso + rodapés: 85,8% do material consumido. Quantitativos estimados para apresentação; conferir gabaritos antes dos cortes.

GABRIEL FERMINO
ARQUITETURA

LUCIANA


PLANO DE CORTE

Placas 900 × 900 mm | Serra: 3 mm | Cortes sem rotação

R06 • OPÇÃO 90 × 90


29 OUT 2026

P110 1 rec.

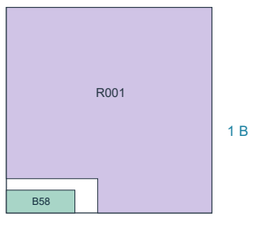


1 B

P111 1 rec.

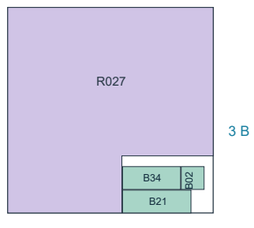


3 B


P112 1 rec.

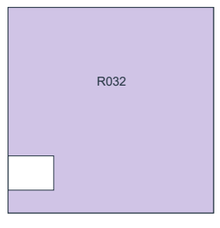

P113 1 rec.

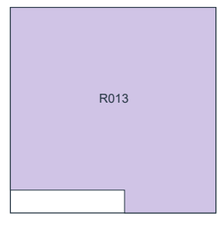


P114 1 rec.

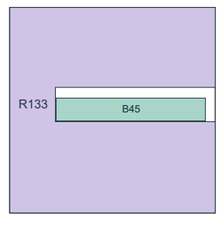


1 B

P115 1 rec.

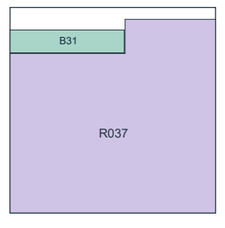

1 B


P116 2 rec.

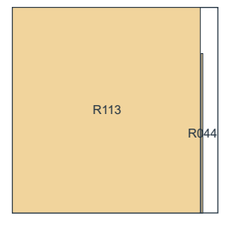


P117 1 rec.




P118 1 rec.

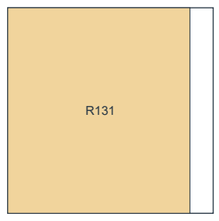


P119 1 rec.

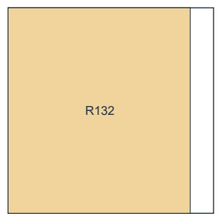


P120 1 rec.

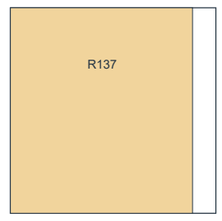


P121 1 rec.

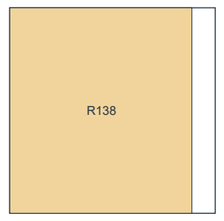


P122 1 rec.

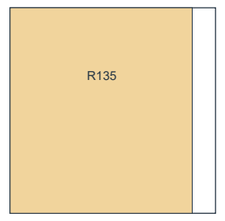


P123 1 rec.

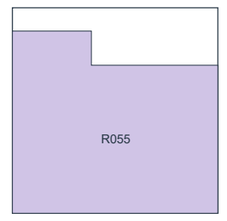

P124 1 rec.

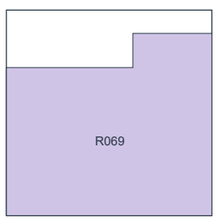


P125 1 rec.

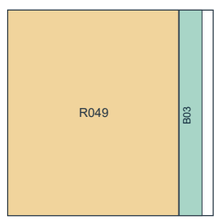


1 B

P126 1 rec.

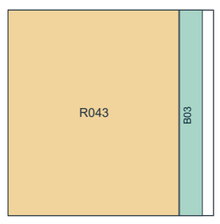


1 B

P127 1 rec.

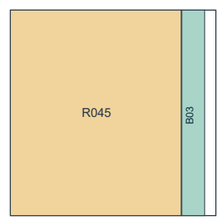


1 B

P128 1 rec.

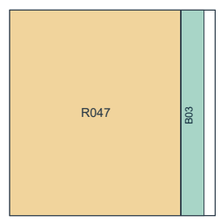


1 B

P129 1 rec.

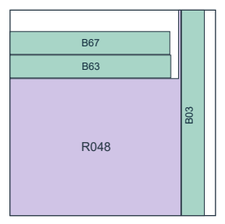


3 B

P130 1 rec.

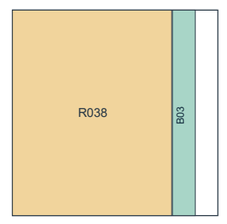


1 B

P131 1 rec.

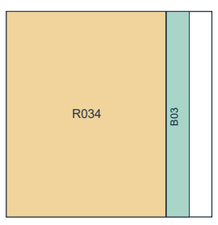


1 B

P132 1 rec.

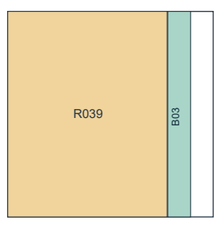


1 B

P133 1 rec.

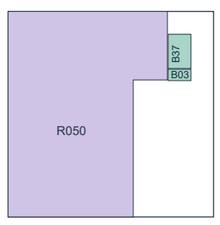


2 B

P134 1 rec.

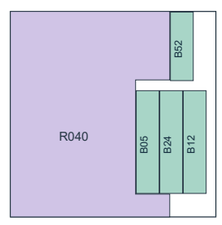


4 B

P135 1 rec.

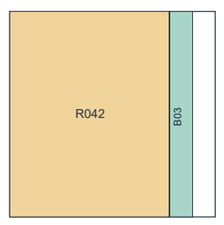


1 B

P136 1 rec.

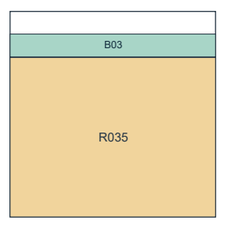


1 B

P137 2 rec.

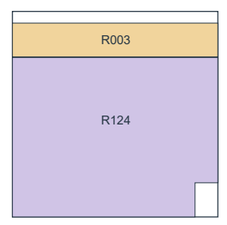


P138 1 rec.

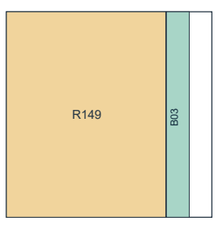


1 B

P139 1 rec.

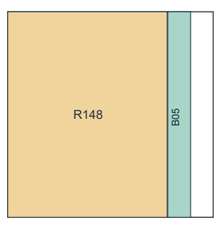


1 B

P140 1 rec.

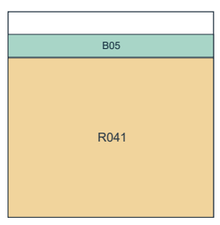


1 B

P141 1 rec.

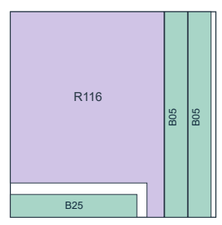


3 B

P142 1 rec.

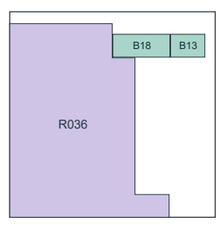


2 B

P143 1 rec.

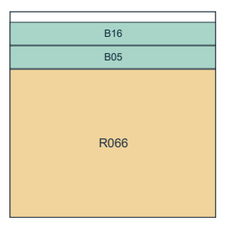


2 B

P144 1 rec.

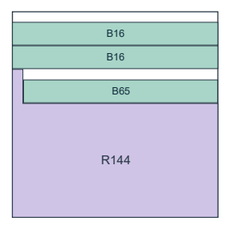


3 B

P145 1 rec.

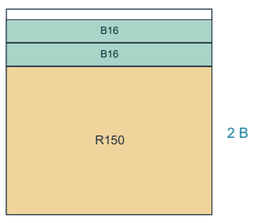


2 B

P146 1 rec.

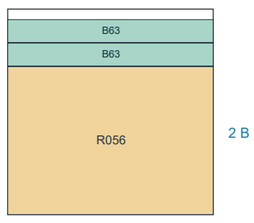


2 B

P147 1 rec.

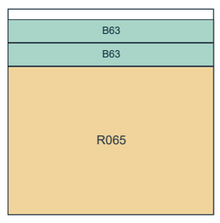


2 B

P148 1 rec.

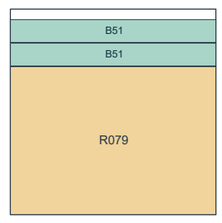


2 B

P149 1 rec.

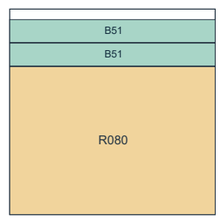


2 B

P150 1 rec.

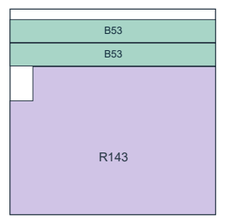


2 B

P151 1 rec.

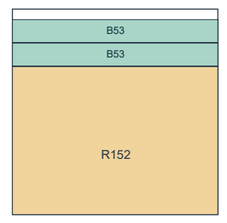


2 B

P152 1 rec.

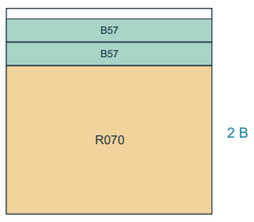


2 B

P153 3 rec.

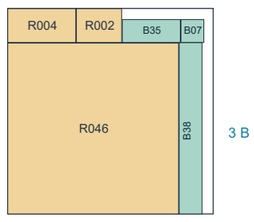


3 B

P154 1 rec.

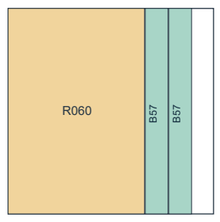


2 B

P155 1 rec.

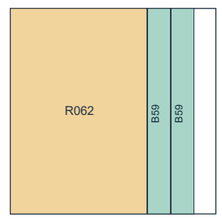


2 B

P156 1 rec.

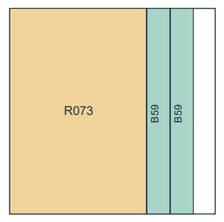


2 B

P157 1 rec.

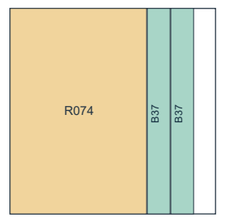


2 B

P158 1 rec.

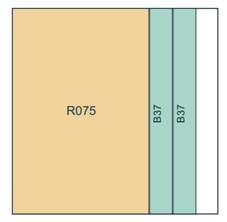


2 B

P159 1 rec.

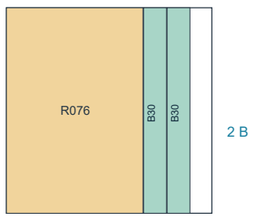


2 B

P160 1 rec.

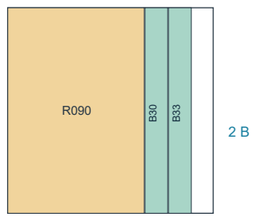


2 B

P161 1 rec.

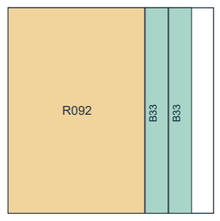

2 B

P162 1 rec.

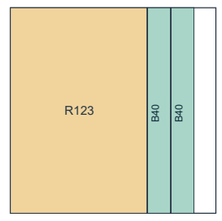


2 B


P163 2 rec.




P164 2 rec.

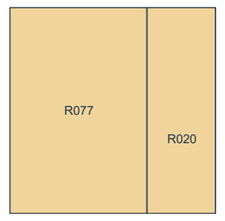

P165 2 rec.

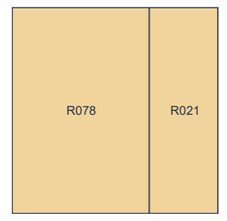

P166 1 rec.

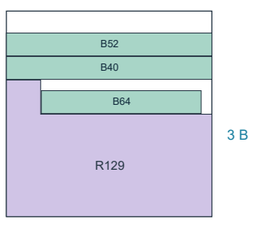


3 B

P167 2 rec.




P168 1 rec.

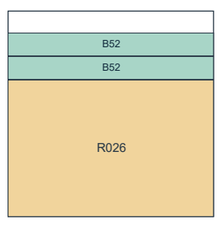


2 B

P169 1 rec.

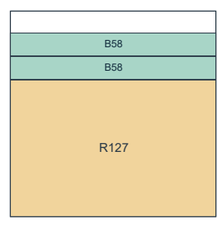


2 B

P170 1 rec.

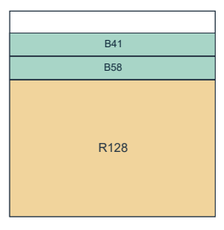


2 B

P171 1 rec.

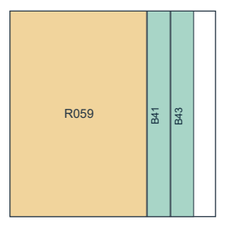


2 B

P172 1 rec.

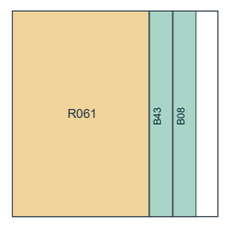


2 B

P173 1 rec.

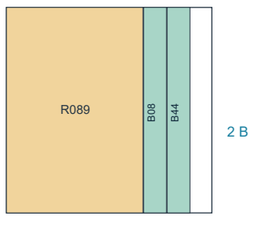


2 B

P174 1 rec.

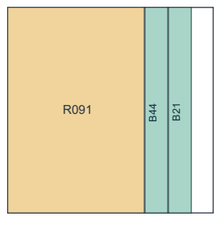


2 B

P175 1 rec.

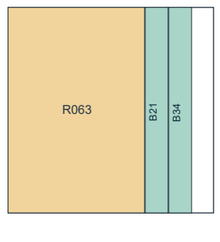


2 B

P176 1 rec.

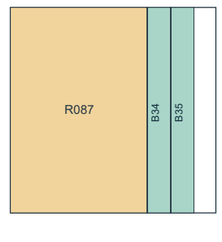


2 B

P177 1 rec.

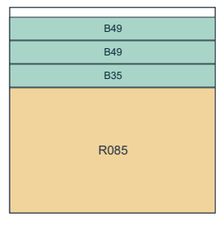


3 B

P178 1 rec.

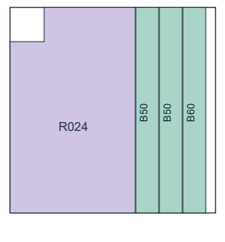

3 B

P179 2 rec.

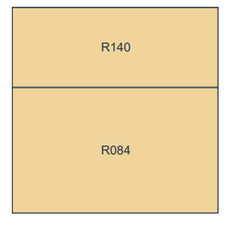

Ocre / lilás: piso | Verde: rodapés Bxx | Branco: sobras e perdas | Lado de cada placa: 0,90 m

GABRIEL FERMINO
ARQUITETURA

LUCIANA


PLANO DE CORTE

Placas 900 × 900 mm | Serra: 3 mm | Cortes sem rotação


R06 • OPÇÃO 90 × 90

29 OUT 2026

P180 2 rec.

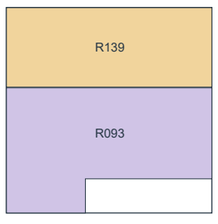


P181 1 rec.

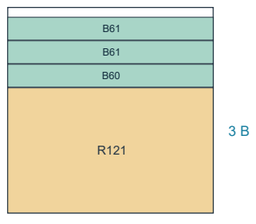


3 B

P182 1 rec.

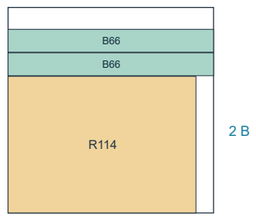


2 B


P183 2 rec.

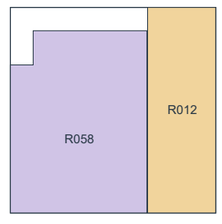

P184 2 rec.

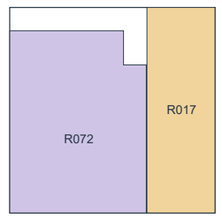


P185 1 rec.

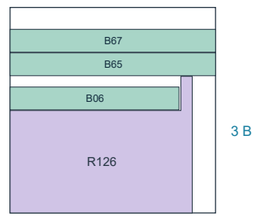


3 B

P186 1 rec.

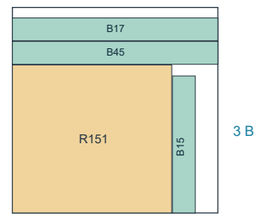


3 B

P187 1 rec.

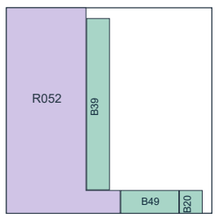


3 B

P188 1 rec.

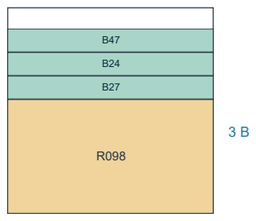


3 B

P189 1 rec.

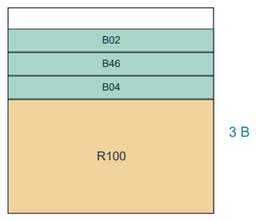


3 B

P190 1 rec.

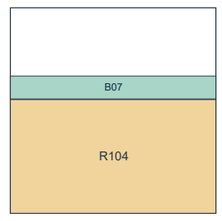


1 B


P191 1 rec.

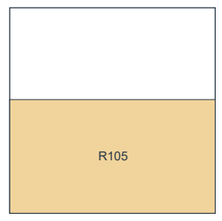

P192 1 rec.

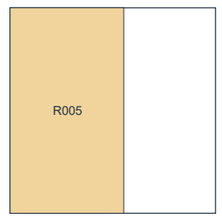

P193 1 rec.

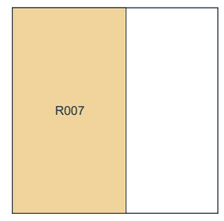


P194 1 rec.




P195 1 rec.




P196 1 rec.

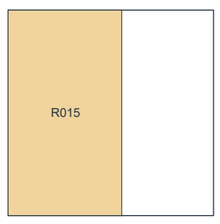


P197 1 rec.

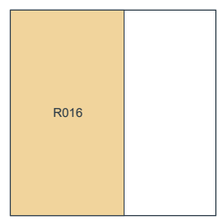


P198 1 rec.

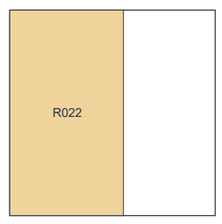

P199 1 rec.

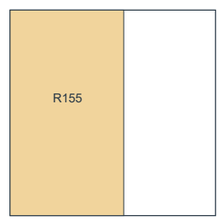


P200 1 rec.

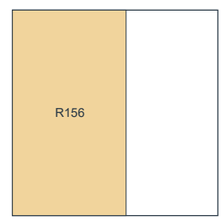

P201 2 rec.




P202 2 rec.

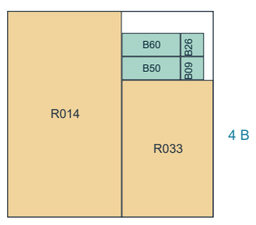


4 B


P203 1 rec.

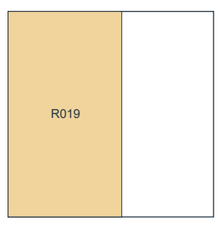


P204 1 rec.

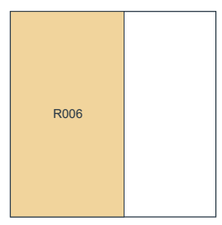


P205 1 rec.

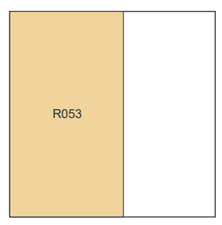

P206 1 rec.

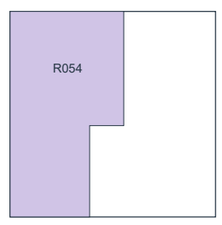

P207 2 rec.

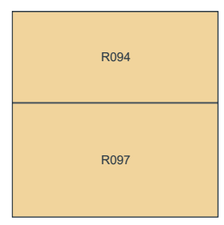


P208 2 rec.



P209 2 rec.




P210 2 rec.

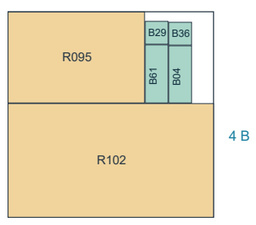


4 B


P211 1 rec.

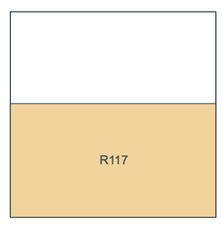


P212 1 rec.

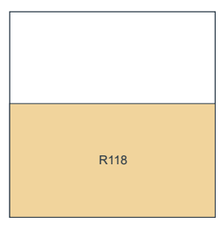


P213 1 rec.

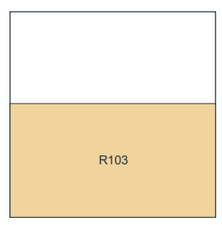


P214 1 rec.

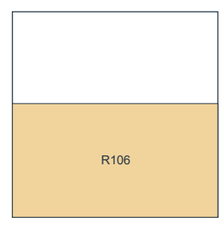


P215 1 rec.

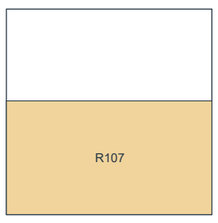

P216 1 rec.

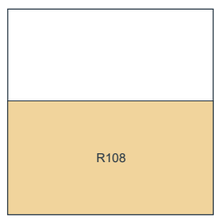

P217 1 rec.

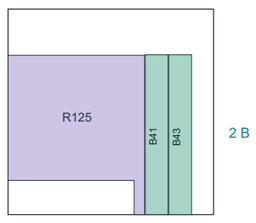


2 B

P218 2 rec.




2 B

P219 1 rec.

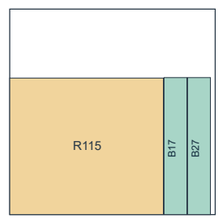


2 B

P220 2 rec.

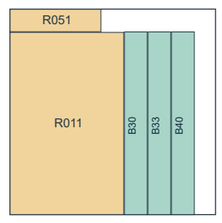


3 B

P221 1 rec.

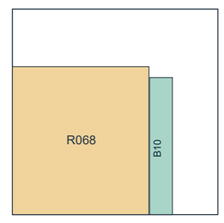


1 B


P222 1 rec.

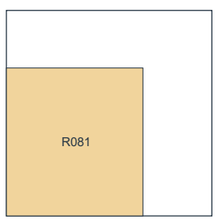


P223 1 rec.

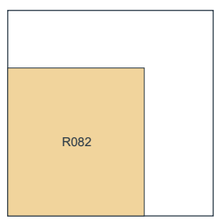


P224 1 rec.

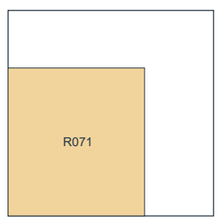


P225 1 rec.

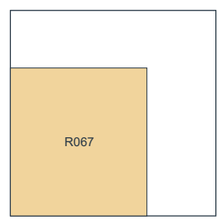


P226 1 rec.

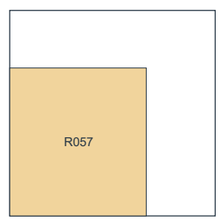

P227 1 rec.

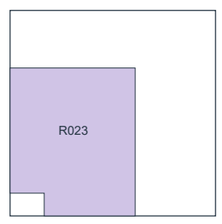


P228 1 rec.

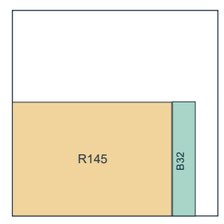


1 B

P229 1 rec.

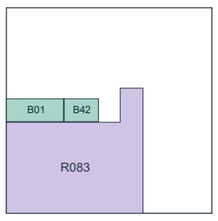


2 B


P230 1 rec.

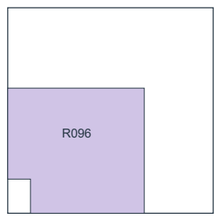

P231 1 rec.

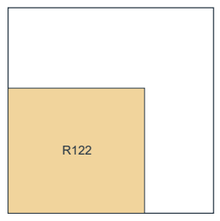


P232 1 rec.

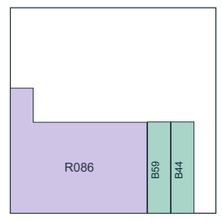


2 B

P233 1 rec.

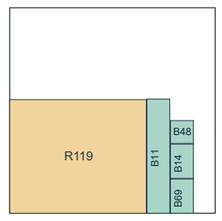


4 B

P234 1 rec.

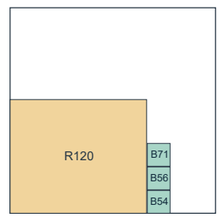


3 B

P235 1 rec.

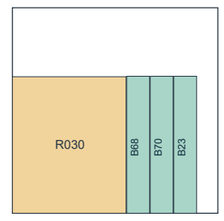


3 B

P236 1 rec.

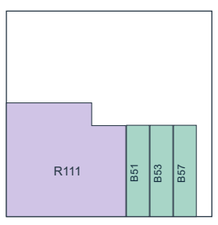

3 B

P237 1 rec.

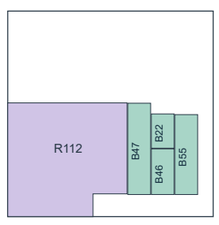


4 B

P238 1 rec.




1 B


P239 1 rec.

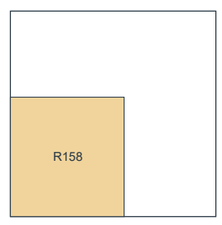


P240 1 rec.

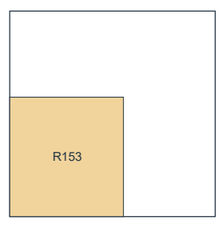


P241 1 rec.

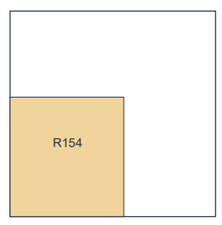


P242 1 rec.

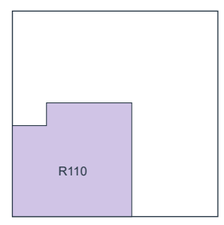


P243 1 rec.

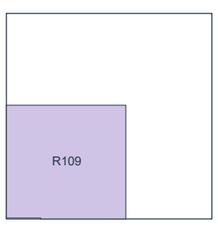


P244 1 rec.

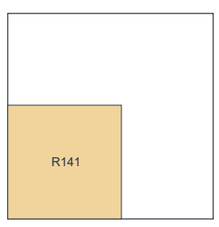


P245 1 rec.

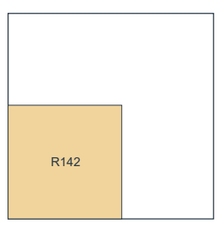

P246 1 rec.

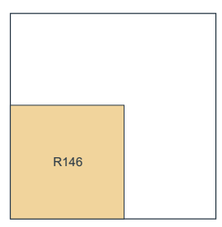

P247 1 rec.

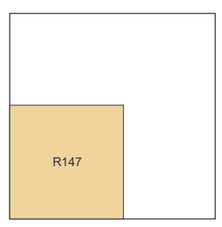

Ocre / lilás: piso | Verde: rodapés Bxx | Branco: sobras e perdas | Lado de cada placa: 0,90 m

GABRIEL FERMINO
ARQUITETURA

LUCIANA

PEÇAS E RODAPÉS

Dimensões dos recortes e rastreio dos rodapés nas placas Pxxx

R06 • OPÇÃO 90 × 90

29 OUT 2026

158 RECORTES | Dimensões envolventes em mm; formatos especiais conforme planta

PEÇA	DIMENSÃO mm	PLACA	TIPO
R001	900,0 × 900,0	P110	ESPECIAL
R002	198,0 × 148,0	P153	RETO
R003	900,0 × 148,0	P137	RETO
R004	298,0 × 148,0	P153	RETO
R005	498,0 × 900,0	P192	RETO
R006	498,0 × 900,0	P204	RETO
R007	498,0 × 900,0	P193	RETO
R008	498,0 × 900,0	P194	RETO
R009	498,0 × 900,0	P195	RETO
R010	298,0 × 900,0	P167	RETO
R011	498,0 × 798,0	P220	RETO
R012	298,0 × 900,0	P183	RETO
R013	900,0 × 900,0	P113	ESPECIAL
R014	498,0 × 900,0	P202	RETO
R015	498,0 × 900,0	P196	RETO
R016	498,0 × 900,0	P197	RETO
R017	298,0 × 900,0	P184	RETO
R018	298,0 × 900,0	P163	RETO
R019	498,0 × 900,0	P203	RETO
R020	298,0 × 900,0	P164	RETO
R021	298,0 × 900,0	P165	RETO
R022	498,0 × 900,0	P198	RETO
R023	548,0 × 648,0	P227	ESPECIAL
R024	548,0 × 900,0	P178	ESPECIAL
R025	398,0 × 900,0	P201	RETO
R026	900,0 × 598,0	P168	RETO
R027	900,0 × 900,0	P111	ESPECIAL
R028	448,0 × 648,0	P218	RETO
R029	498,0 × 900,0	P201	RETO
R030	498,0 × 598,0	P235	RETO
R031	448,0 × 900,0	P218	ESPECIAL
R032	900,0 × 900,0	P112	ESPECIAL
R033	398,0 × 598,0	P202	RETO
R034	698,0 × 900,0	P131	RETO
R035	900,0 × 698,0	P136	RETO
R036	698,0 × 848,0	P142	ESPECIAL
R037	900,0 × 848,0	P115	ESPECIAL
R038	698,0 × 900,0	P130	RETO
R039	698,0 × 900,0	P132	RETO
R040	698,0 × 900,0	P134	ESPECIAL
R041	900,0 × 698,0	P140	RETO
R042	698,0 × 900,0	P135	RETO
R043	748,0 × 900,0	P126	RETO
R044	8,0 × 698,0	P116	RETO
R045	748,0 × 900,0	P127	RETO
R046	748,0 × 748,0	P153	RETO
R047	748,0 × 900,0	P128	RETO
R048	748,0 × 900,0	P129	ESPECIAL
R049	748,0 × 900,0	P125	RETO
R050	698,0 × 900,0	P133	ESPECIAL
R051	398,0 × 98,0	P220	RETO
R052	498,0 × 900,0	P187	ESPECIAL
R053	498,0 × 900,0	P205	RETO
R054	498,0 × 900,0	P206	ESPECIAL
R055	900,0 × 798,0	P123	ESPECIAL
R056	900,0 × 648,0	P146	RETO
R057	598,0 × 648,0	P226	RETO
R058	598,0 × 798,0	P183	ESPECIAL
R059	598,0 × 900,0	P171	RETO
R060	598,0 × 900,0	P154	RETO
R061	598,0 × 900,0	P172	RETO
R062	598,0 × 900,0	P155	RETO
R063	598,0 × 900,0	P175	RETO
R064	598,0 × 900,0	P163	RETO
R065	900,0 × 648,0	P147	RETO
R066	900,0 × 648,0	P143	RETO
R067	598,0 × 648,0	P225	RETO
R068	598,0 × 648,0	P221	RETO
R069	900,0 × 798,0	P124	ESPECIAL
R070	900,0 × 648,0	P152	RETO
R071	598,0 × 648,0	P224	RETO
R072	598,0 × 798,0	P184	ESPECIAL
R073	598,0 × 900,0	P156	RETO
R074	598,0 × 900,0	P157	RETO
R075	598,0 × 900,0	P158	RETO
R076	598,0 × 900,0	P159	RETO
R077	598,0 × 900,0	P164	RETO
R078	598,0 × 900,0	P165	RETO
R079	900,0 × 648,0	P148	RETO
R080	900,0 × 648,0	P149	RETO
R081	598,0 × 648,0	P222	RETO
R082	598,0 × 648,0	P223	RETO
R083	598,0 × 548,0	P229	ESPECIAL
R084	900,0 × 548,0	P179	RETO
R085	900,0 × 548,0	P177	RETO
R086	598,0 × 548,0	P232	ESPECIAL
R087	598,0 × 900,0	P176	RETO
R088	598,0 × 900,0	P167	RETO
R089	598,0 × 900,0	P173	RETO
R090	598,0 × 900,0	P160	RETO
R091	598,0 × 900,0	P174	RETO
R092	598,0 × 900,0	P161	RETO
R093	900,0 × 548,0	P180	ESPECIAL
R094	900,0 × 398,0	P207	RETO
R095	598,0 × 398,0	P210	RETO
R096	598,0 × 548,0	P230	ESPECIAL
R097	900,0 × 498,0	P207	RETO
R098	900,0 × 498,0	P188	RETO
R099	900,0 × 498,0	P208	RETO
R100	900,0 × 498,0	P189	RETO
R101	900,0 × 498,0	P209	RETO
R102	900,0 × 498,0	P210	RETO
R103	900,0 × 498,0	P213	RETO
R104	900,0 × 498,0	P190	RETO
R105	900,0 × 498,0	P191	RETO
R106	900,0 × 498,0	P214	RETO
R107	900,0 × 498,0	P215	RETO
R108	900,0 × 498,0	P216	RETO
R109	523,0 × 498,0	P243	ESPECIAL
R110	523,0 × 498,0	P242	ESPECIAL
R111	523,0 × 498,0	P236	ESPECIAL
R112	523,0 × 498,0	P237	ESPECIAL
R113	823,0 × 900,0	P116	RETO
R114	823,0 × 598,0	P182	RETO
R115	673,0 × 598,0	P219	RETO
R116	673,0 × 900,0	P141	ESPECIAL
R117	900,0 × 498,0	P211	RETO
R118	900,0 × 498,0	P212	RETO
R119	598,0 × 498,0	P233	RETO
R120	598,0 × 498,0	P234	RETO
R121	900,0 × 548,0	P181	RETO
R122	598,0 × 548,0	P231	RETO
R123	598,0 × 900,0	P162	RETO
R124	900,0 × 698,0	P137	ESPECIAL
R125	598,0 × 698,0	P217	ESPECIAL
R126	798,0 × 598,0	P185	ESPECIAL
R127	900,0 × 598,0	P169	RETO
R128	900,0 × 598,0	P170	RETO
R129	900,0 × 598,0	P166	ESPECIAL
R130	798,0 × 900,0	P117	RETO
R131	798,0 × 900,0	P118	RETO
R132	798,0 × 900,0	P119	RETO
R133	900,0 × 900,0	P114	ESPECIAL
R134	900,0 × 398,0	P209	RETO
R135	798,0 × 900,0	P122	RETO
R136	900,0 × 398,0	P208	RETO
R137	798,0 × 900,0	P120	RETO
R138	798,0 × 900,0	P121	RETO
R139	900,0 × 348,0	P180	RETO
R140	900,0 × 348,0	P179	RETO
R141	498,0 × 498,0	P244	RETO
R142	498,0 × 498,0	P245	RETO
R143	900,0 × 648,0	P150	ESPECIAL
R144	900,0 × 648,0	P144	ESPECIAL
R145	698,0 × 498,0	P228	RETO
R146	498,0 × 498,0	P246	RETO
R147	498,0 × 498,0	P247	RETO
R148	698,0 × 900,0	P139	RETO
R149	698,0 × 900,0	P138	RETO
R150	900,0 × 648,0	P145	RETO
R151	698,0 × 648,0	P186	RETO
R152	900,0 × 648,0	P151	RETO
R153	498,0 × 523,0	P240	RETO
R154	498,0 × 523,0	P241	RETO
R155	498,0 × 900,0	P199	RETO
R156	498,0 × 900,0	P200	RETO
R157	498,0 × 523,0	P238	RETO
R158	498,0 × 523,0	P239	RETO

INTEIRAS: I01 a I109, 900 × 900 mm. R001 a R158: recortes. Conferir contornos por gabarito.

RODAPÉS 10 CM | 111,84 M | 163 PEÇAS APROVEITADAS

TRECHO	METROS	PEÇAS	PLACAS DE ORIGEM
B01	0,250	1	229
B02	1,000	2	111/189
B03	9,950	12	125/126/127/128/129/130/131/132/133/135/136/138
B04	1,150	2	189/210
B05	4,950	6	134/139/140/141/143
B06	0,740	1	185
B07	1,000	2	153/190
B08	2,314	3	172/173/238
B09	0,100	1	202
B10	0,600	1	221
B11	0,500	1	233
B12	0,450	1	134
B13	0,150	1	142
B14	0,150	1	233
B15	0,600	1	186
B16	4,500	5	143/144/145
B17	1,500	2	186/219
B18	0,250	1	142
B19	0,150	1	218
B20	0,100	1	187
B21	2,100	3	111/174/175
B22	0,150	1	237
B23	0,600	1	235
B24	1,350	2	134/188
B25	0,554	1	141
B26	0,100	1	202
B27	1,500	2	188/219
B28	0,250	1	218
B29	0,100	1	210
B30	3,500	4	159/160/220
B31	0,500	1	115
B32	0,500	1	228
B33	3,500	4	160/161/220
B34	2,054	3	111/175/176
B35	2,054	3	153/176/177
B36	0,100	1	210
B37	3,750	5	133/157/158
B38	0,750	1	153
B39	0,750	1	187
B40	3,500	4	162/166/220
B41	2,500	3	170/171/217
B42	0,150	1	229
B43	2,500	3	171/172/217
B44	2,200	3	173/174/232
B45	1,554	2	114/186
B46	1,100	2	189/237
B47	1,300	2	188/237
B48	0,100	1	233
B49	2,054	3	177/187
B50	2,054	3	178/202
B51	4,000	5	148/149/236
B52	3,000	4	134/166/168
B53	4,000	5	150/151/236
B54	0,100	1	234
B55	0,350	1	237
B56	0,100	1	234
B57	4,000	5	152/154/236
B58	3,000	4	110/169/170
B59	4,000	5	155/156/232
B60	2,054	3	178/181/202
B61	2,054	3	181/210
B63	4,304	5	129/146/147
B64	0,700	1	166
B65	1,750	2	144/185
B66	1,800	2	182
B67	1,600	2	129/185
B68	0,600	1	235
B69	0,150	1	233
B70	0,600	1	235
B71	0,100	1	234

Bxx identifica o trecho de parede; os mapas P02/P03 mostram a placa de origem. Comprimentos geométricos: ajustar os rejuntes dos rodapés no assentamento.