
GABRIEL FERMINO
ARQUITETURA

LUCIANA

PAGINAÇÃO DE PISOS

York WH NAT 120 × 120 | Rejunte: 2 mm | Pavimento superior

PLANTA DE ASSENTAMENTO E RODAPÉS | 1:75

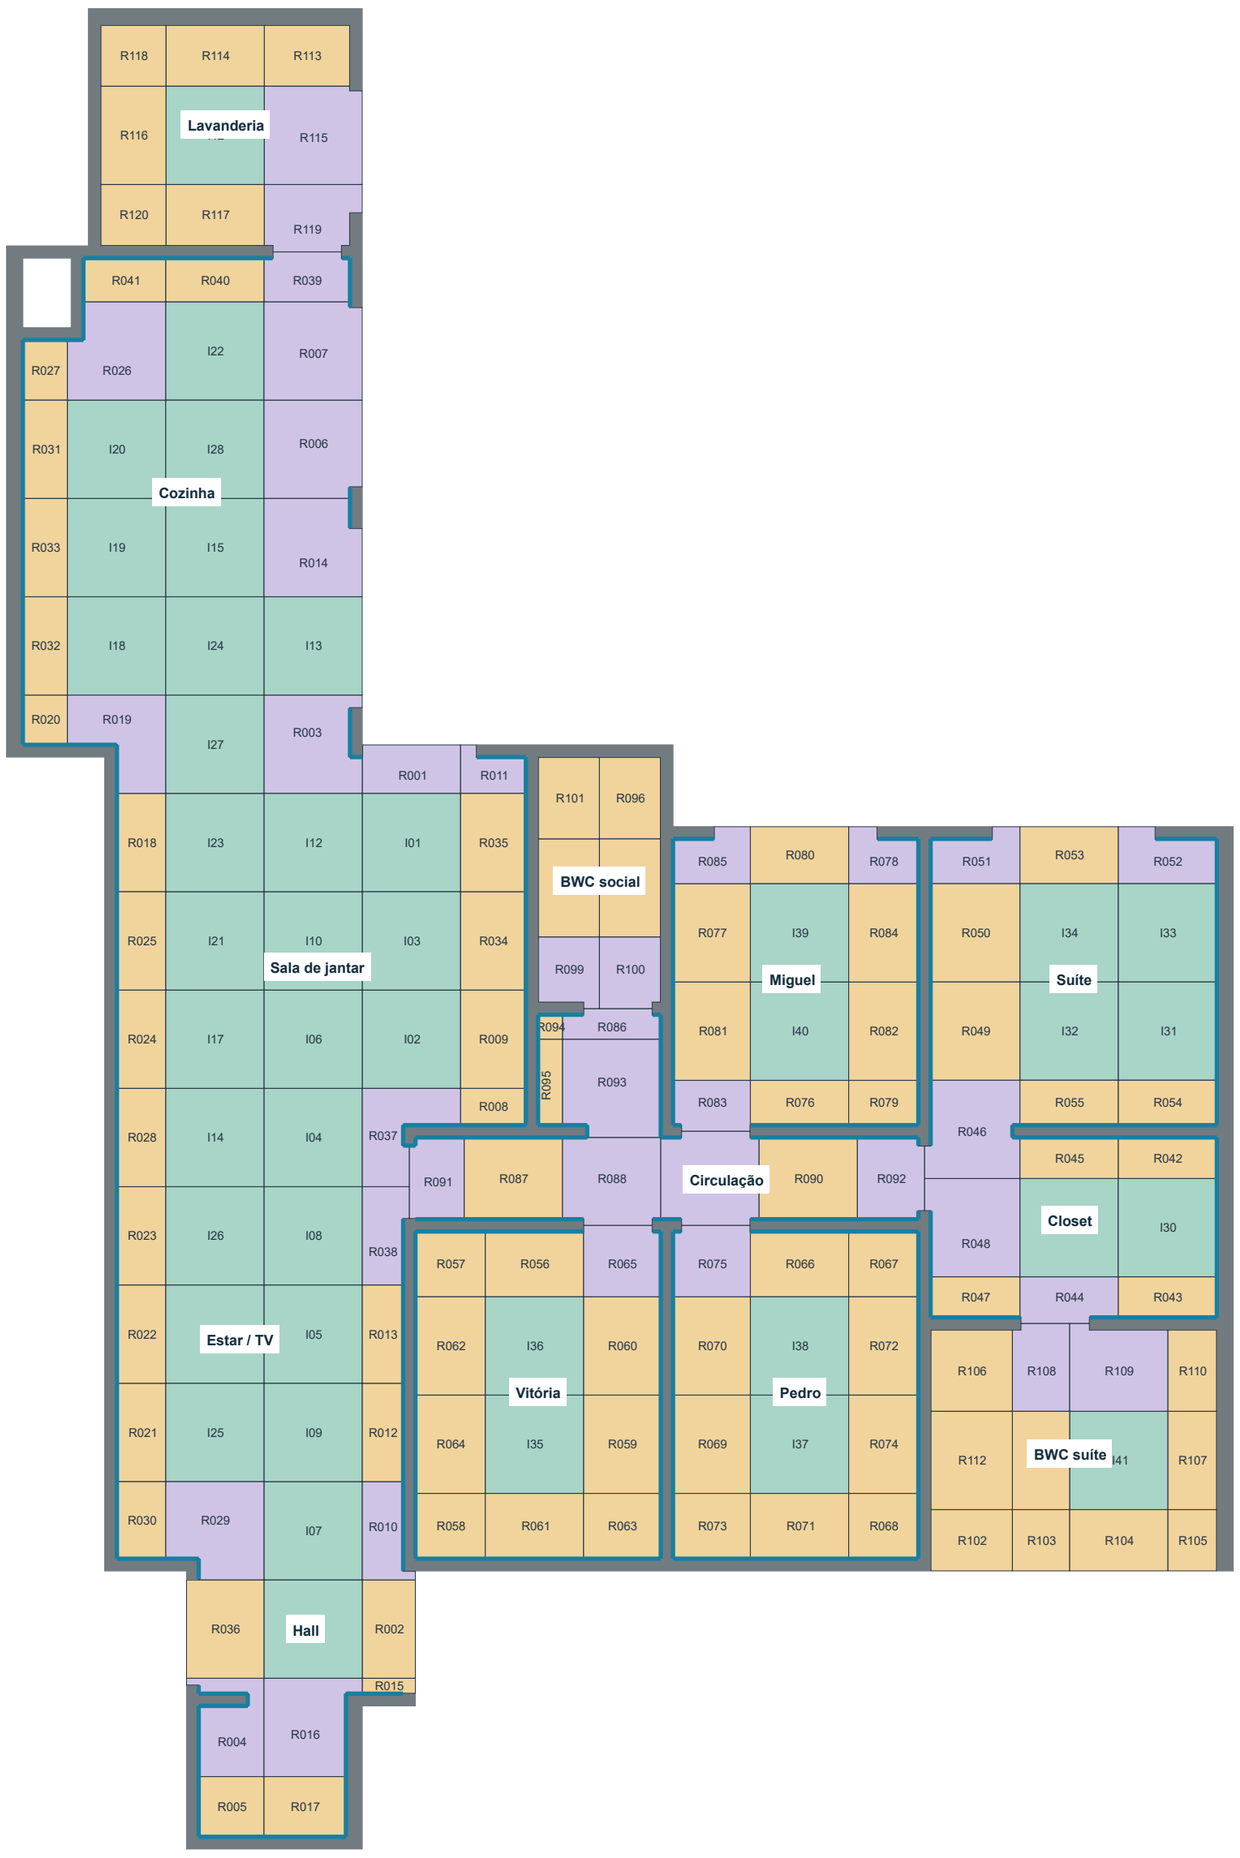

Inteira 1200 × 1200

Recorte retangular

Recorte especial / em L

Rodapé de 10 cm

Circulação livre: 0,95 m, sem filetes laterais

0 1 2 3 4 5 m

PISO LÍQUIDO	RODAPÉ 10 CM
159,60 m²	111,84 m

QUANTITATIVO POR AMBIENTE

AMBIENTE	INT.	REC.	m²	ROD. m
Social integrado	28	41	72,68	41,83
Suíte + closet	6	14	20,36	20,05
Quarto Miguel	2	10	10,78	10,15
Quarto Vitória	2	10	11,96	13,15
Quarto Pedro	2	10	11,96	13,15
Circulação	0	10	8,60	13,49
BWC social	0	6	4,51	-
BWC suíte	1	11	10,31	-
Lavanderia	1	8	8,45	-
TOTAL	**42**	**120**	**159,60**	**111,84**

CONSUMO E COMPRA

Placas inteiras	42
Placas para os recortes	94
Consumo total	136 placas | 195,84 m²
Reserva	8 placas | 11,52 m²
COMPRA	**144 placas | 207,36 m²**

Compra: 72 caixas de 2,88 m² ou 144 caixas de 1,44 m². Confirmar embalagem e lote.

APROVEITAMENTO

Rodapés: 11,18 m², em 134 peças, retiradas das sobras do piso. Nenhuma placa adicional no plano de corte.

Separar e identificar os retalhos conforme P02 e P03. Sem reaproveitamento, os rodapés exigem outras 9 placas antes da reserva.

DIRETRIZES DE ASSENTAMENTO

Malha contínua entre cozinha, sala de jantar, TV e hall; malha contínua entre suíte e closet. Nos dormitórios, recortes concentrados no lado previsto para cama e criados.

Rejunte: 2 mm. Folga perimetral: 5 mm. Peças nominais: 1200 × 1200 mm. Conferir dimensões reais e esquadros antes dos cortes.

Rodapés sem banheiros e lavanderia, descontados os vãos e as ombreiras. Marcenaria não descontada. Revestimentos de parede não incluídos.

Piso + rodapés aproveitados: 87,2% do material consumido. A reserva de compra está separada do consumo.

CORTE E EXECUÇÃO

Serra considerada: 3 mm. Manter o sentido das peças do piso, sem rotação de 90°. Recortes em L: transferir por gabarito e conferir os cantos internos.

Conferir em obra ralos, caimentos e juntas estruturais e de movimentação. A faixa R015, no hall junto ao jardim, mede 18,2 cm.

Índice: P01 planta e quantitativos; P02 e P03 cortes e aproveitamento; P04 dimensões dos recortes e origem dos rodapés. Imprimir a 100%.


GABRIEL FERMINO
ARQUITETURA

LUCIANA

PLANO DE CORTE


Placas 1200 × 1200 mm | Serra: 3 mm | Cortes sem rotação

P043 1 rec.

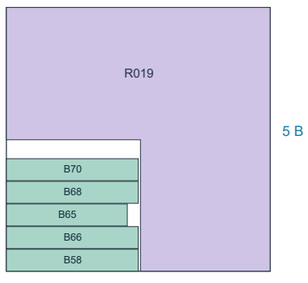


5 B

P044 1 rec.

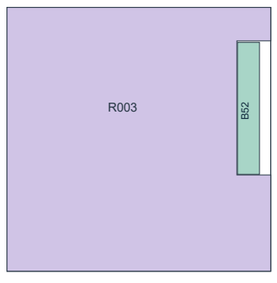


1 B

P045 1 rec.

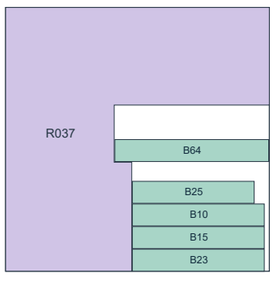


5 B

P046 1 rec.

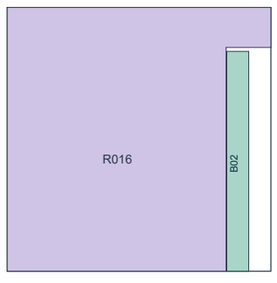


1 B

P047 1 rec.

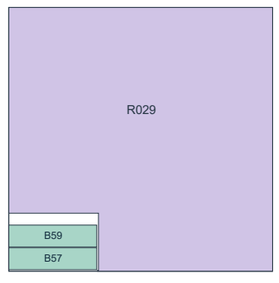


2 B

P048 1 rec.

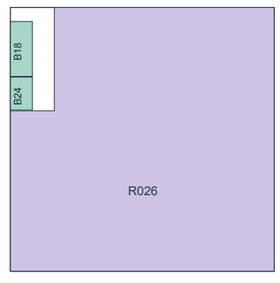


2 B

P049 1 rec.

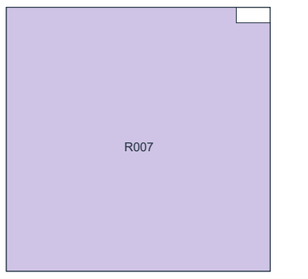


P050 1 rec.

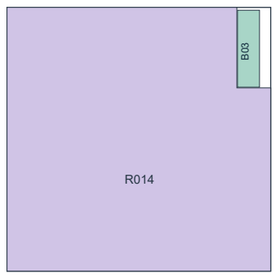


1 B


P051 1 rec.

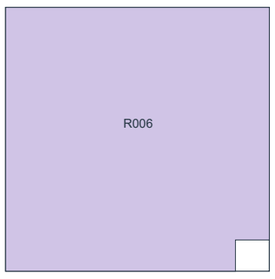

P052 1 rec.

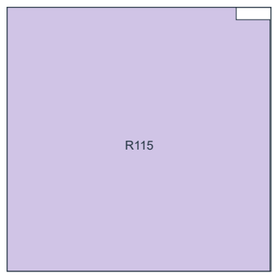


P053 1 rec.

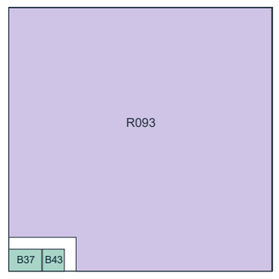


2 B


P054 1 rec.

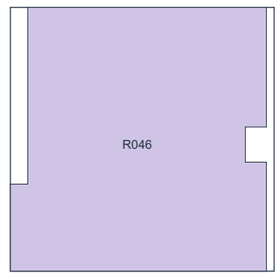


P055 1 rec.

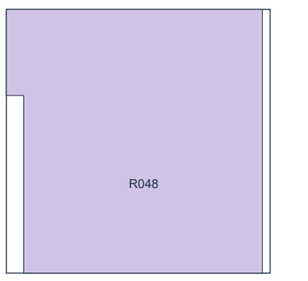

P056 1 rec.

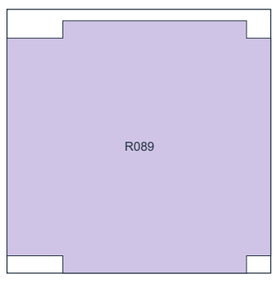


P057 1 rec.

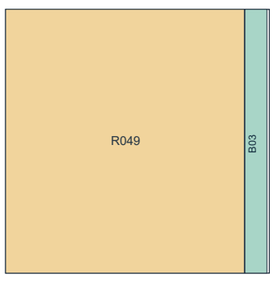


1 B

P058 1 rec.

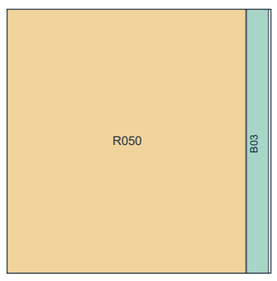


1 B

P059 1 rec.

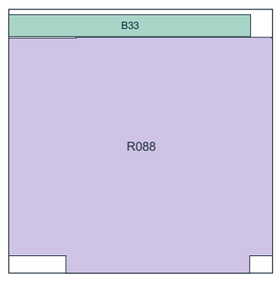


1 B

P060 1 rec.

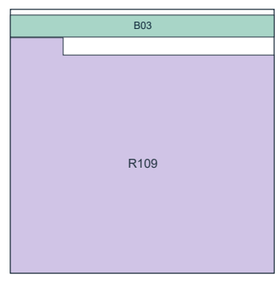


1 B

P061 1 rec.

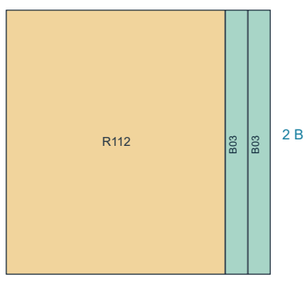


2 B

P062 1 rec.

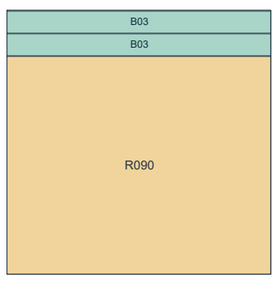


2 B

P063 1 rec.

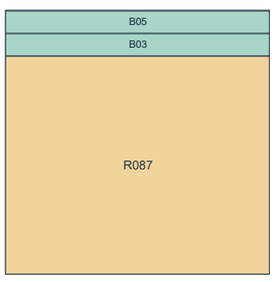


2 B

P064 1 rec.

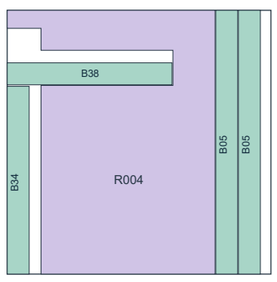


4 B

P065 1 rec.

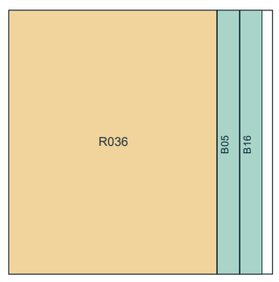


2 B

P066 1 rec.

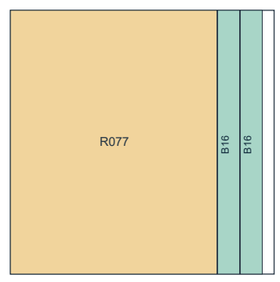


2 B

P067 1 rec.

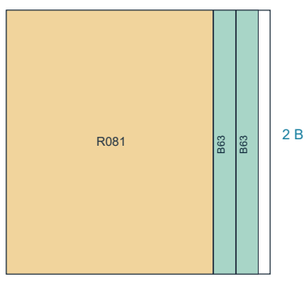


2 B

P068 1 rec.

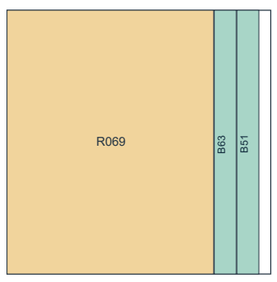


2 B

P069 1 rec.

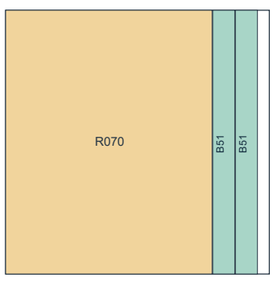


2 B

P070 1 rec.

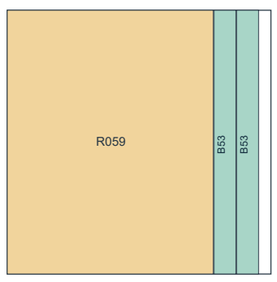


2 B

P071 1 rec.

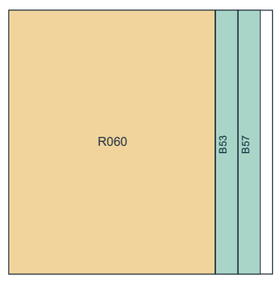


2 B

P072 2 rec.

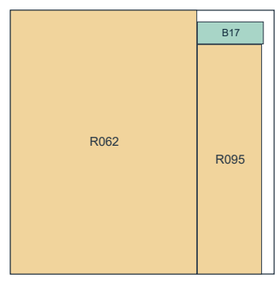


1 B

P073 1 rec.

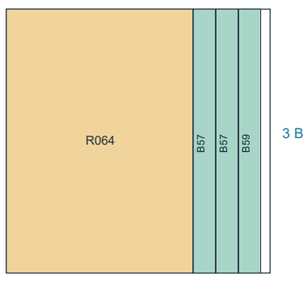


3 B

P074 1 rec.

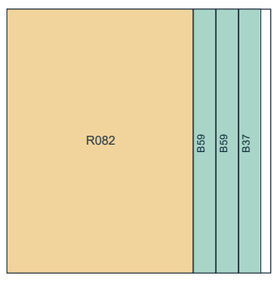


3 B

P075 1 rec.

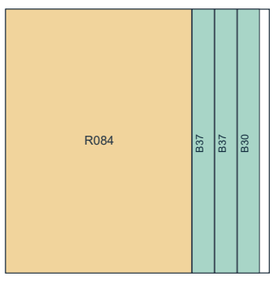


3 B

P076 1 rec.

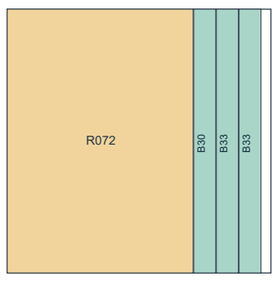


3 B

P077 1 rec.

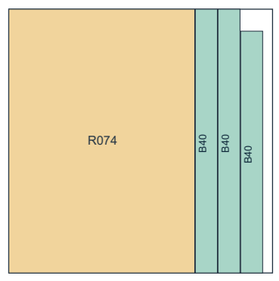


3 B

P078 1 rec.

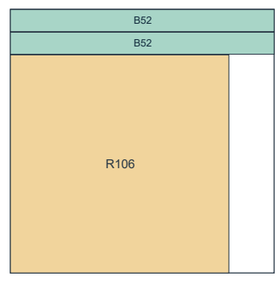


2 B

P079 2 rec.

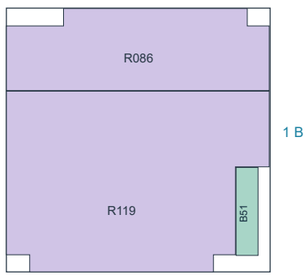


1 B

P080 1 rec.

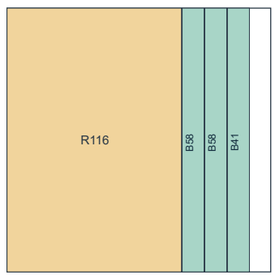


3 B

P081 1 rec.

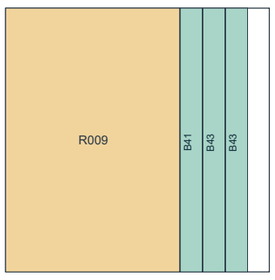


3 B

P082 1 rec.

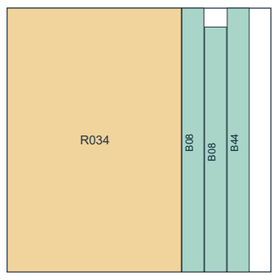


3 B

P083 1 rec.

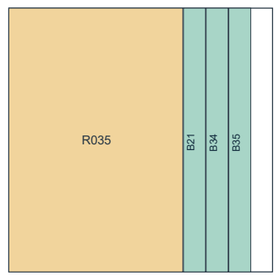


3 B

P084 1 rec.

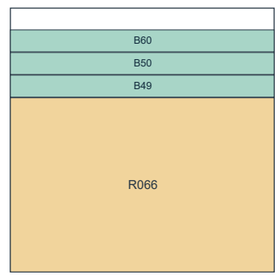


3 B

P085 1 rec.

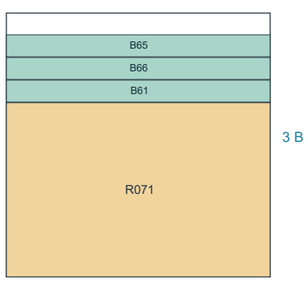


3 B

P086 1 rec.

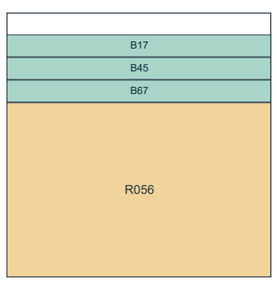


3 B

P087 1 rec.

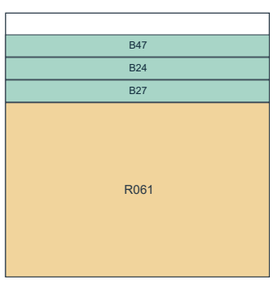


3 B

P088 1 rec.

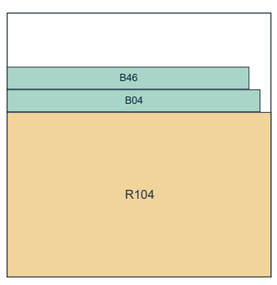


2 B

P089 1 rec.

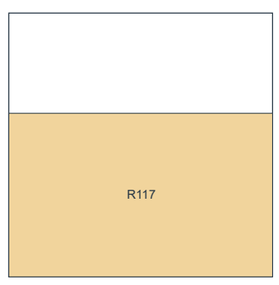

P090 1 rec.

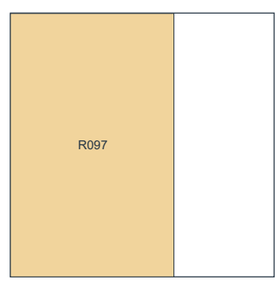

Ocre / lilás: piso | Verde: rodapés Bxx | Branco: sobras e perdas | Lado de cada placa: 1,20 m

GABRIEL FERMINO
ARQUITETURA

LUCIANA


PLANO DE CORTE

Placas 1200 × 1200 mm | Serra: 3 mm | Cortes sem rotação

P091 1 rec.



P092 1 rec.

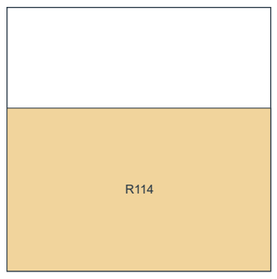


P093 2 rec.




P094 2 rec.




P095 1 rec.

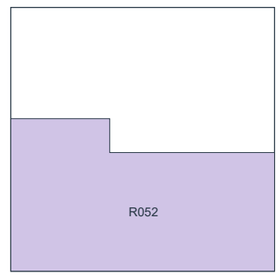


P096 1 rec.

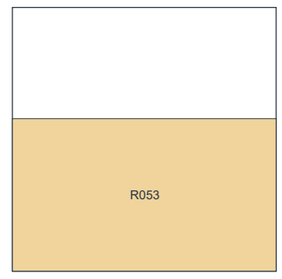


P097 1 rec.

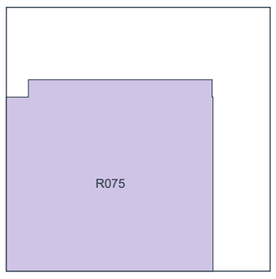


P098 1 rec.

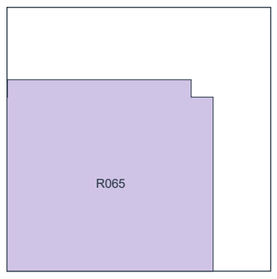


P099 1 rec.

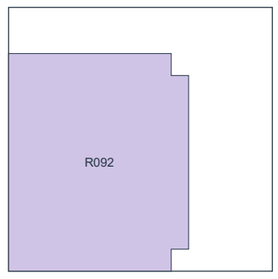


P100 2 rec.

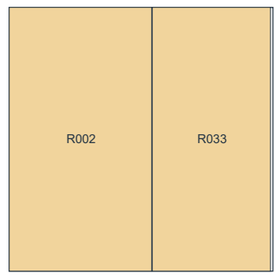


P101 2 rec.

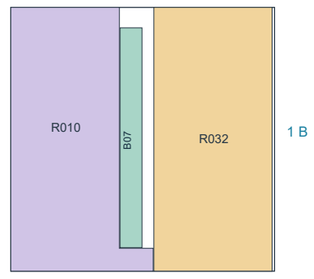


P102 1 rec.

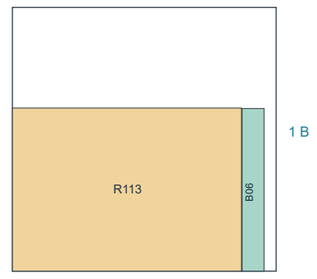


P103 2 rec.

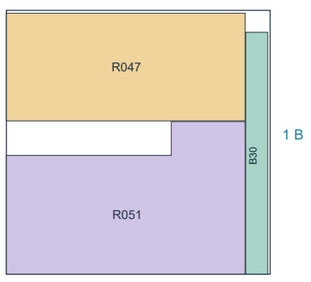


P104 2 rec.

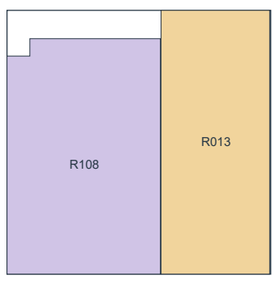


P105 1 rec.

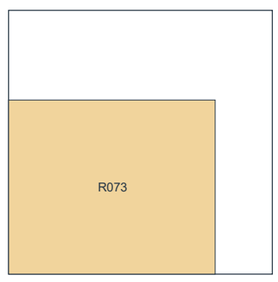


P106 3 rec.

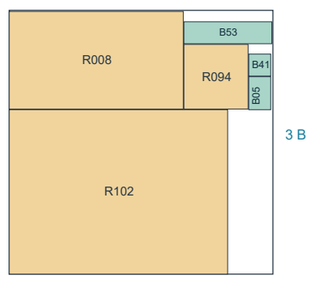


P107 1 rec.

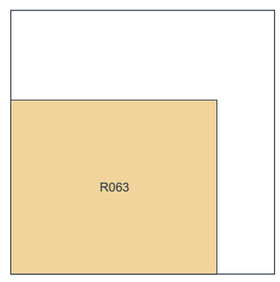


P108 1 rec.

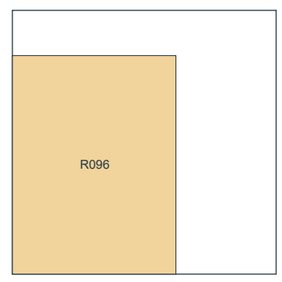


P109 1 rec.

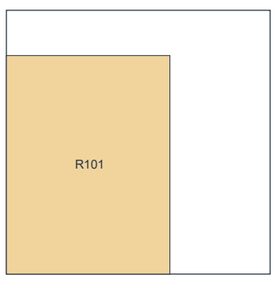

P110 1 rec.

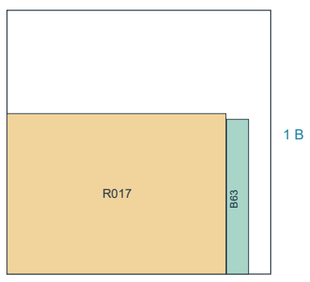


P111 2 rec.

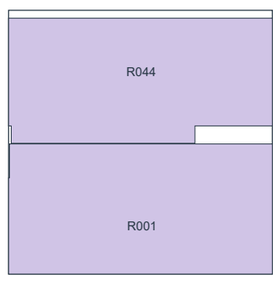


P112 2 rec.



P113 2 rec.

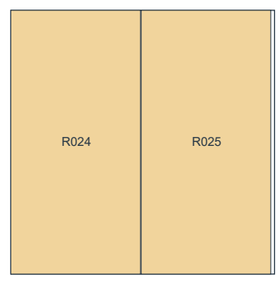


P114 2 rec.

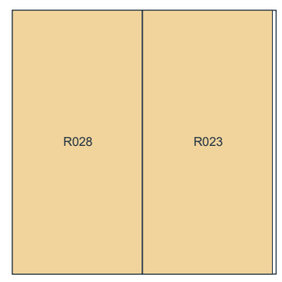


P115 2 rec.




P116 2 rec.

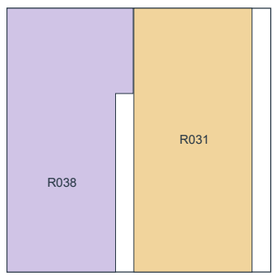


P117 1 rec.

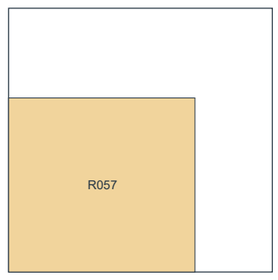


P118 1 rec.

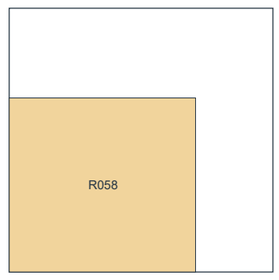


P119 1 rec.

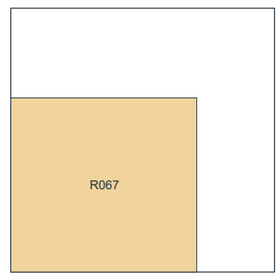


P120 1 rec.

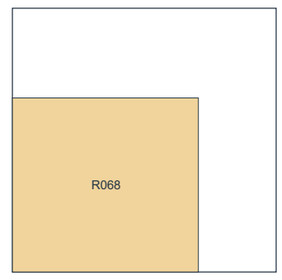


P121 2 rec.

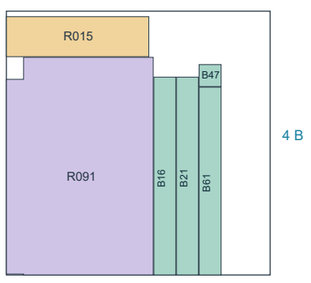


P122 2 rec.

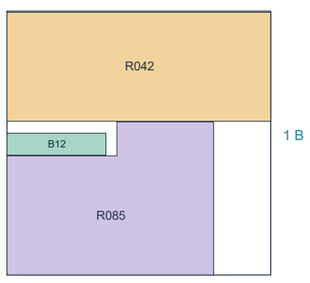


P123 2 rec.

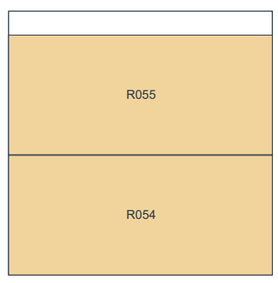


P124 2 rec.

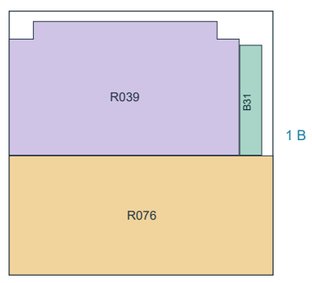


P125 1 rec.

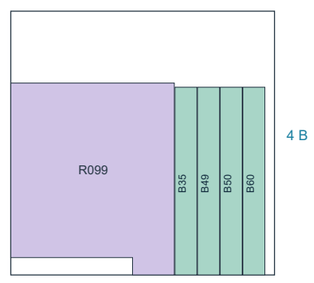


P126 1 rec.

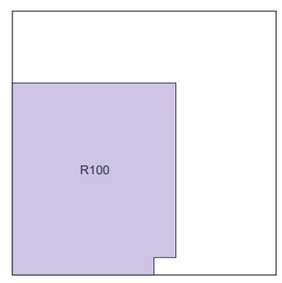


P127 2 rec.

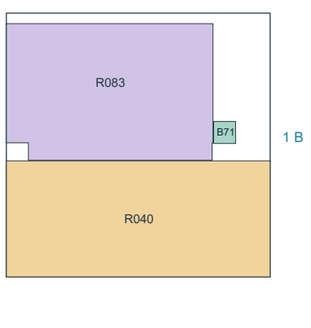


P128 1 rec.

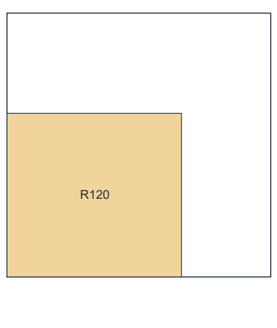


P129 1 rec.

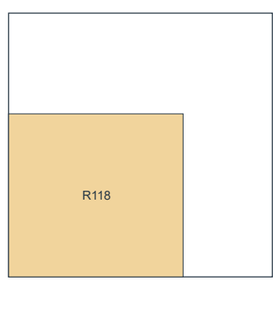


P130 2 rec.

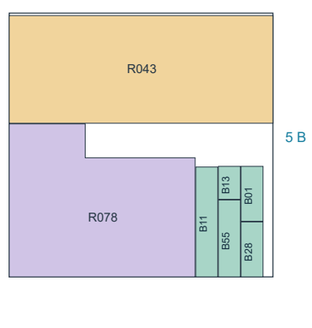


P131 2 rec.

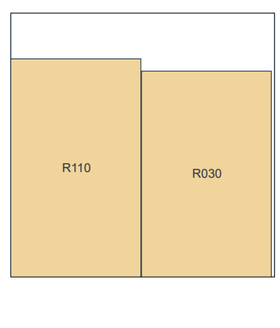


P132 1 rec.

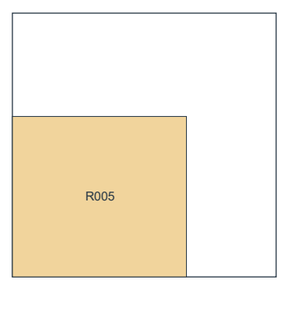


P133 2 rec.

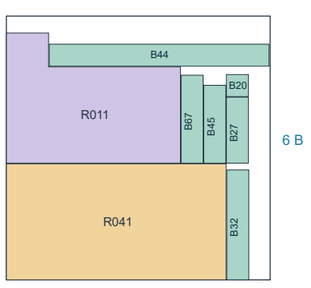


P134 1 rec.

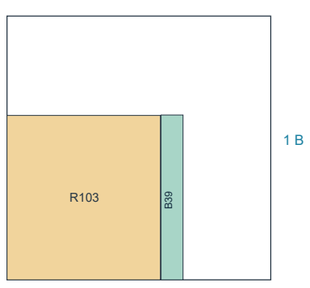

P135 2 rec.

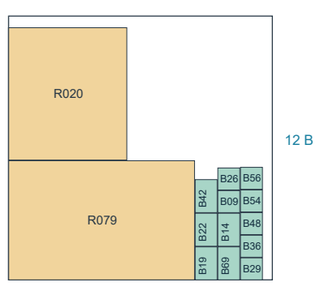

P136 2 rec.

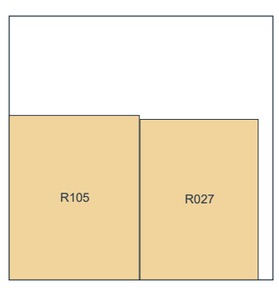

Ocre / lilás: piso | Verde: rodapés Bxx | Branco: sobras e perdas | Lado de cada placa: 1,20 m

GABRIEL FERMINO
ARQUITETURA

LUCIANA

PEÇAS E RODAPÉS

Dimensões dos recortes e rastreio dos rodapés nas placas Pxxx

120 RECORTES | Dimensões envolventes em mm; formatos especiais conforme planta

PEÇA	DIMENSÃO mm	PLACA	TIPO
R001	1.200,0 × 592,0	P111	ESPECIAL
R002	648,0 × 1.200,0	P100	RETO
R003	1.200,0 × 1.200,0	P044	ESPECIAL
R004	946,0 × 1.200,0	P064	ESPECIAL
R005	792,0 × 730,0	P132	RETO
R006	1.200,0 × 1.200,0	P051	ESPECIAL
R007	1.200,0 × 1.200,0	P049	ESPECIAL
R008	792,0 × 444,0	P106	RETO
R009	792,0 × 1.200,0	P081	RETO
R010	648,0 × 1.200,0	P101	ESPECIAL
R011	792,0 × 592,0	P133	ESPECIAL
R012	494,0 × 1.200,0	P093	RETO
R013	494,0 × 1.200,0	P104	RETO
R014	1.200,0 × 1.200,0	P050	ESPECIAL
R015	648,0 × 182,0	P121	RETO
R016	1.200,0 × 1.200,0	P046	ESPECIAL
R017	996,0 × 730,0	P110	RETO
R018	590,0 × 1.200,0	P112	RETO
R019	1.200,0 × 1.200,0	P043	ESPECIAL
R020	538,0 × 602,0	P135	RETO
R021	590,0 × 1.200,0	P115	RETO
R022	590,0 × 1.200,0	P115	RETO
R023	590,0 × 1.200,0	P114	RETO
R024	590,0 × 1.200,0	P113	RETO
R025	590,0 × 1.200,0	P113	RETO
R026	1.200,0 × 1.200,0	P048	ESPECIAL
R027	538,0 × 730,0	P136	RETO
R028	590,0 × 1.200,0	P114	RETO
R029	1.200,0 × 1.200,0	P047	ESPECIAL
R030	590,0 × 936,0	P131	RETO
R031	538,0 × 1.200,0	P116	RETO
R032	538,0 × 1.200,0	P101	RETO
R033	538,0 × 1.200,0	P100	RETO
R034	792,0 × 1.200,0	P082	RETO
R035	792,0 × 1.200,0	P083	RETO
R036	946,0 × 1.200,0	P065	RETO
R037	1.200,0 × 1.200,0	P045	ESPECIAL
R038	574,0 × 1.200,0	P116	ESPECIAL
R039	1.046,0 × 608,0	P124	ESPECIAL
R040	1.200,0 × 528,0	P127	RETO
R041	1.000,0 × 528,0	P133	RETO
R042	1.200,0 × 496,0	P122	RETO
R043	1.200,0 × 490,0	P130	RETO
R044	1.200,0 × 569,0	P111	ESPECIAL
R045	1.200,0 × 496,0	P094	RETO
R046	1.165,0 × 1.200,0	P054	ESPECIAL
R047	1.086,0 × 490,0	P103	RETO
R048	1.165,0 × 1.200,0	P055	ESPECIAL
R049	1.086,0 × 1.200,0	P057	RETO
R050	1.086,0 × 1.200,0	P058	RETO
R051	1.086,0 × 694,0	P103	ESPECIAL
R052	1.200,0 × 694,0	P095	ESPECIAL
R053	1.200,0 × 694,0	P096	RETO
R054	1.200,0 × 544,0	P123	RETO
R055	1.200,0 × 544,0	P123	RETO
R056	1.200,0 × 792,0	P086	RETO
R057	848,0 × 792,0	P117	RETO
R058	848,0 × 792,0	P118	RETO
R059	938,0 × 1.200,0	P070	RETO
R060	938,0 × 1.200,0	P071	RETO
R061	1.200,0 × 792,0	P087	RETO
R062	848,0 × 1.200,0	P072	RETO
R063	938,0 × 792,0	P107	RETO
R064	848,0 × 1.200,0	P073	RETO
R065	938,0 × 871,0	P098	ESPECIAL
R066	1.200,0 × 792,0	P084	RETO
R067	846,0 × 792,0	P119	RETO
R068	846,0 × 792,0	P120	RETO
R069	940,0 × 1.200,0	P068	RETO
R070	940,0 × 1.200,0	P069	RETO
R071	1.200,0 × 792,0	P085	RETO
R072	846,0 × 1.200,0	P076	RETO
R073	940,0 × 792,0	P105	RETO
R074	846,0 × 1.200,0	P077	RETO
R075	940,0 × 871,0	P097	ESPECIAL
R076	1.200,0 × 542,0	P124	RETO
R077	940,0 × 1.200,0	P066	RETO
R078	846,0 × 696,0	P130	ESPECIAL
R079	846,0 × 542,0	P135	RETO
R080	1.200,0 × 696,0	P094	RETO
R081	940,0 × 1.200,0	P067	RETO
R082	846,0 × 1.200,0	P074	RETO
R083	940,0 × 621,0	P127	ESPECIAL
R084	846,0 × 1.200,0	P075	RETO
R085	940,0 × 696,0	P122	ESPECIAL
R086	1.196,0 × 373,0	P079	ESPECIAL
R087	1.200,0 × 990,0	P063	RETO
R088	1.200,0 × 1.073,0	P059	ESPECIAL
R089	1.200,0 × 1.148,0	P056	ESPECIAL
R090	1.200,0 × 990,0	P062	RETO
R091	668,0 × 990,0	P121	ESPECIAL
R092	819,0 × 990,0	P099	ESPECIAL
R093	1.196,0 × 1.198,0	P053	ESPECIAL
R094	292,0 × 294,0	P106	RETO
R095	292,0 × 1.044,0	P072	RETO
R096	744,0 × 994,0	P108	RETO
R097	744,0 × 1.198,0	P090	RETO
R098	744,0 × 1.198,0	P091	RETO
R099	744,0 × 873,0	P125	ESPECIAL
R100	744,0 × 873,0	P126	ESPECIAL
R101	744,0 × 994,0	P109	RETO
R102	994,0 × 748,0	P106	RETO
R103	698,0 × 748,0	P134	RETO
R104	1.200,0 × 748,0	P088	RETO
R105	592,0 × 748,0	P136	RETO
R106	994,0 × 992,0	P078	RETO
R107	592,0 × 1.200,0	P112	RETO
R108	698,0 × 1.071,0	P104	ESPECIAL
R109	1.200,0 × 1.071,0	P060	ESPECIAL
R110	592,0 × 992,0	P131	RETO
R111	698,0 × 1.200,0	P093	RETO
R112	994,0 × 1.200,0	P061	RETO
R113	1.042,0 × 742,0	P102	RETO
R114	1.200,0 × 742,0	P092	RETO
R115	1.196,0 × 1.200,0	P052	ESPECIAL
R116	794,0 × 1.200,0	P080	RETO
R117	1.200,0 × 744,0	P089	RETO
R118	794,0 × 742,0	P129	RETO
R119	1.196,0 × 822,0	P079	ESPECIAL
R120	794,0 × 744,0	P128	RETO

INTEIRAS: I01 a I42, 1200 × 1200 mm. R001 a R120: recortes. Conferir contornos por gabarito.

RODAPÉS 10 CM | 111,84 M | 134 PEÇAS APROVEITADAS

TRECHO	METROS	PEÇAS	PLACAS DE ORIGEM
B01	0,250	1	130
B02	1,000	1	46
B03	9,950	9	50/57/58/60/61/62/63
B04	1,150	1	88
B05	4,950	5	63/64/65/106
B06	0,740	1	102
B07	1,000	1	101
B08	2,314	2	82
B09	0,100	1	135
B10	0,600	1	45
B11	0,500	1	130
B12	0,450	1	122
B13	0,150	1	130
B14	0,150	1	135
B15	0,600	1	45
B16	4,500	4	65/66/121
B17	1,500	2	72/86
B18	0,250	1	48
B19	0,150	1	135
B20	0,100	1	133
B21	2,100	2	83/121
B22	0,150	1	135
B23	0,600	1	45
B24	1,350	2	48/87
B25	0,554	1	45
B26	0,100	1	135
B27	1,500	2	87/133
B28	0,250	1	130
B29	0,100	1	135
B30	3,500	3	75/76/103
B31	0,500	1	124
B32	0,500	1	133
B33	3,500	3	59/76
B34	2,054	2	64/83
B35	2,054	2	83/125
B36	0,100	1	135
B37	3,750	4	53/74/75
B38	0,750	1	64
B39	0,750	1	134
B40	3,500	3	77
B41	2,500	3	80/81/106
B42	0,150	1	135
B43	2,500	3	53/81
B44	2,200	2	82/133
B45	1,554	2	86/133
B46	1,100	1	88
B47	1,300	2	87/121
B48	0,100	1	135
B49	2,054	2	84/125
B50	2,054	2	84/125
B51	4,000	4	68/69/79
B52	3,000	3	44/78
B53	4,000	4	70/71/106
B54	0,100	1	135
B55	0,350	1	130
B56	0,100	1	135
B57	4,000	4	47/71/73
B58	3,000	3	43/80
B59	4,000	4	47/73/74
B60	2,054	2	84/125
B61	2,054	2	85/121
B63	4,304	4	67/68/110
B64	0,700	1	45
B65	1,750	2	43/85
B66	1,800	2	43/85
B67	1,600	2	86/133
B68	0,600	1	43
B69	0,150	1	135
B70	0,600	1	43
B71	0,100	1	127

Bxx identifica o trecho de parede; os mapas P02/P03 mostram a placa de origem. Comprimentos geométricos: ajustar os rejuntes dos rodapés no assentamento.