GABRIEL FERMINO
ARQUITETURA


LUCIANA

BANHEIRO SUÍTE | PAREDES

Portinari Paraná Gold 120 × 120 cm | Rejunte: 2 mm

ELEVAÇÕES INTERNAS | ESCALA 1:20

PAREDE A - BOX

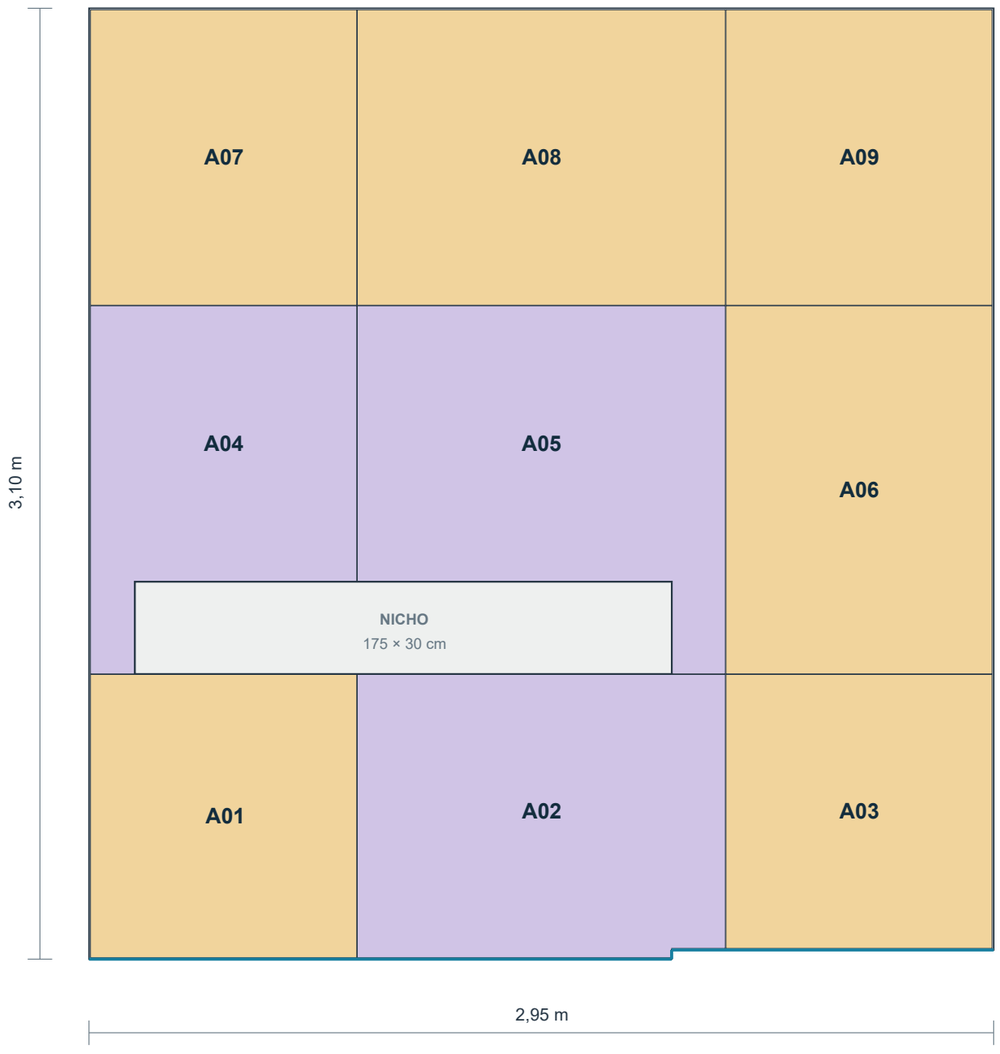

PAREDE B - PORTA



Box: cota -0,03 m | restante: cota 0,00 m.

Nicho: base +0,90 m (+0,93 m sobre o box).

Nicho proposto: início a 7 cm do canto A/B.

Deslocamento de +2 cm; dimensões mantidas.

Topo comum: +3,07 m | altura a partir do box: 3,10 m | juntas horizontais alinhadas nas duas paredes.

Recorte reto | Recorte especial / em L | Abertura / outro acabamento

PARANÁ GOLD | ÁREAS LÍQUIDAS DAS PAREDES

PAREDE	ÁREA BRUTA	PORTA	NICHOS	ÁREA LÍQUIDA
Parede A - box	9,11 m²	0,00 m²	0,52 m²	8,59 m²
Parede B - porta	10,74 m²	1,83 m²	0,27 m²	8,65 m²
TOTAL LÍQUIDO PARANÁ GOLD				**17,24 m²**

Área líquida das paredes: descontados porta, nichos e piso fora do box. Fundos, laterais e soleiras dos nichos excluídos.

PEDRA MOLEDO | SOMENTE QUANTITATIVO

Face completa, antes do nicho	15,85 m²
Desconto do nicho (280 × 30 cm)	0,84 m²
ÁREA LÍQUIDA	**15,01 m²**

Inclui toda a face marcada no modelo, com a continuação de 1,50 m e o trecho superior até a cota +4,50 m. Sem paginação e sem acréscimo de perdas da pedra.

CONSUMO DE PLACAS E RESERVA

Peças instaladas	21 recortes
Placas no plano de corte	17 | 24,48 m²
Reserva de obra / manutenção	1 placa | 1,44 m²
COMPRA PREVISTA	**18 placas | 25,92 m²**

O quantitativo de compra vem dos recortes e da reserva, não apenas da área líquida. Confirmar embalagem, calibre e lote antes da aquisição.

DEFINIÇÕES PARA EXECUÇÃO

Rejunte de 2 mm; folgas perimetrais de 5 mm; serra de 3 mm. Manter o sentido das peças e conferir os veios antes dos cortes. A fiada central mede 1,20 m; as fiadas inferior e superior absorvem os arremates.

Nicho B proposto 2 cm mais afastado do canto: recorte lateral útil de 6,3 cm. Conferir medidas acabadas, impermeabilização e gabaritos. As juntas de encontro devem receber o tratamento indicado para áreas molhadas.

GABRIEL FERMINO
ARQUITETURA


LUCIANA

CORTES E PEÇAS


Paraná Gold 120 × 120 cm | Identificação Axx / Bxx por parede

PLANO DE CORTE E APROVEITAMENTO | PLACAS DE 1,20 × 1,20 M


P01 1 rec.

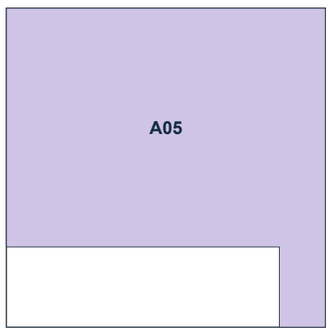


P02 1 rec.

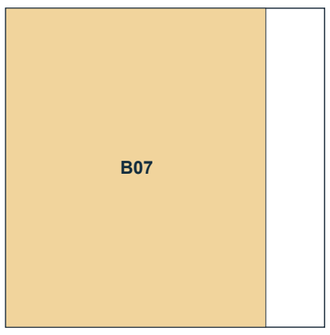


P03 1 rec.

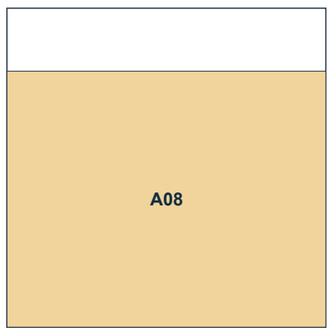


P04 1 rec.

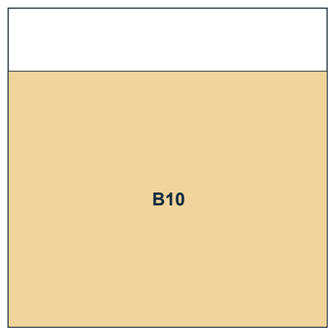


P05 1 rec.

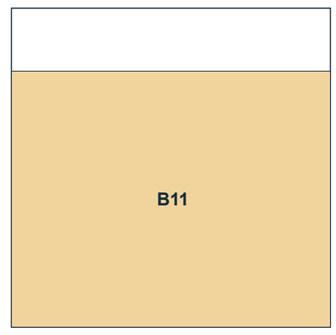


P06 1 rec.

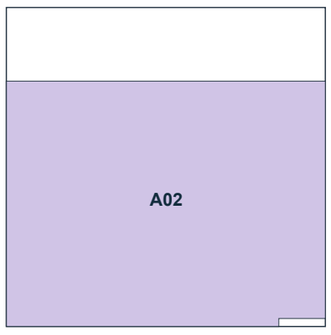


P07 1 rec.

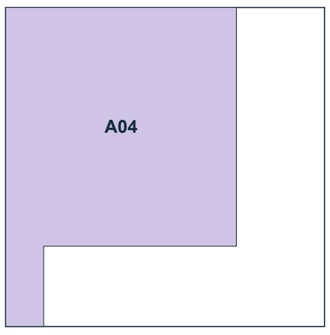


P08 1 rec.

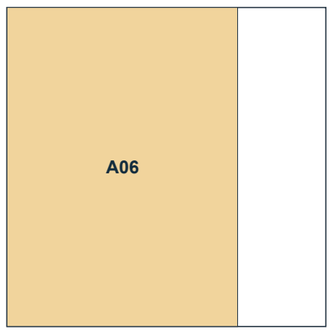


P09 1 rec.

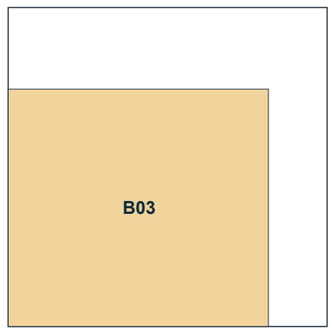


P10 1 rec.

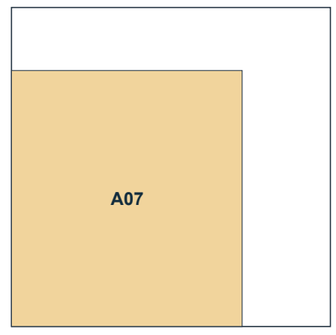


P11 1 rec.

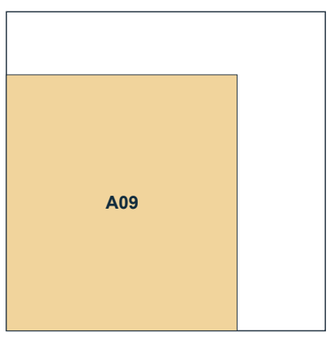


P12 1 rec.

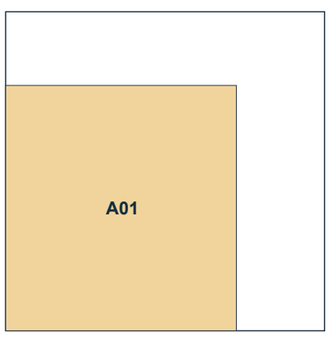


P13 1 rec.

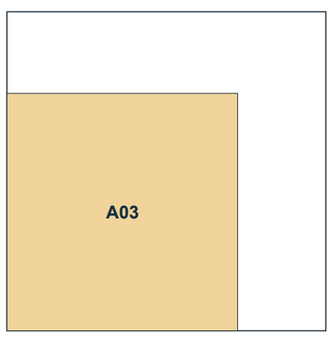


P14 2 rec.

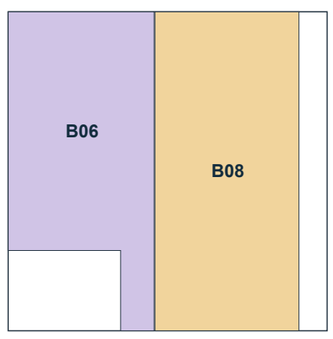


P15 2 rec.

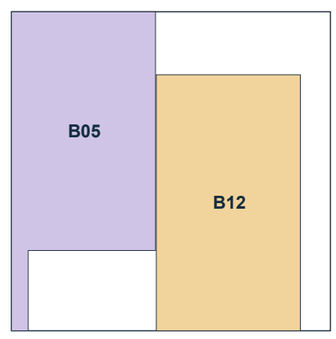

P16 2 rec.

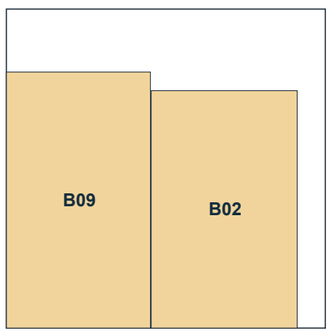

P17 2 rec.

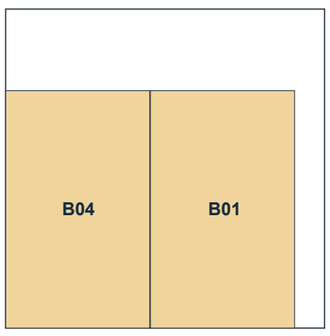

Branco: retalhos remanescentes / perda de corte. Peças sem rotação de 90°. A reserva de uma placa não está desenhada.

LISTA DE PEÇAS | DIMENSÕES ENVOLVENTES EM MILÍMETROS

PEÇA	DIMENSÃO mm	PLACA	TIPO
A01	868 × 923	P12	RETO
A02	1.200 × 923	P06	ESPECIAL
A03	868 × 893	P13	RETO
A04	868 × 1.200	P07	ESPECIAL
A05	1.200 × 1.200	P01	ESPECIAL
A06	868 × 1.200	P08	RETO
A07	868 × 963	P10	RETO
A08	1.200 × 963	P03	RETO
A09	868 × 963	P11	RETO
B01	542 × 893	P17	RETO
B02	549 × 893	P16	RETO

PEÇA	DIMENSÃO mm	PLACA	TIPO
B03	979 × 893	P09	RETO
B04	542 × 893	P17	RETO
B05	542 × 1.200	P15	ESPECIAL
B06	549 × 1.200	P14	ESPECIAL
B07	979 × 1.200	P02	RETO
B08	542 × 1.200	P14	RETO
B09	542 × 963	P16	RETO
B10	1.200 × 963	P04	RETO
B11	1.200 × 963	P05	RETO
B12	542 × 963	P15	RETO

As dimensões listadas são os retângulos envolventes. Manter os contornos em L e os recortes de nichos e porta conforme as elevações. Executar gabaritos antes de cortar as placas; o plano admite apenas as sobras identificadas.

Nicho A: 175 × 30 cm. Nicho B: 90 × 30 cm, com deslocamento proposto de +2 cm. Não incluídos fundos e retornos dos nichos. Referência de corte: Manual Portinari, seção 1.11.